



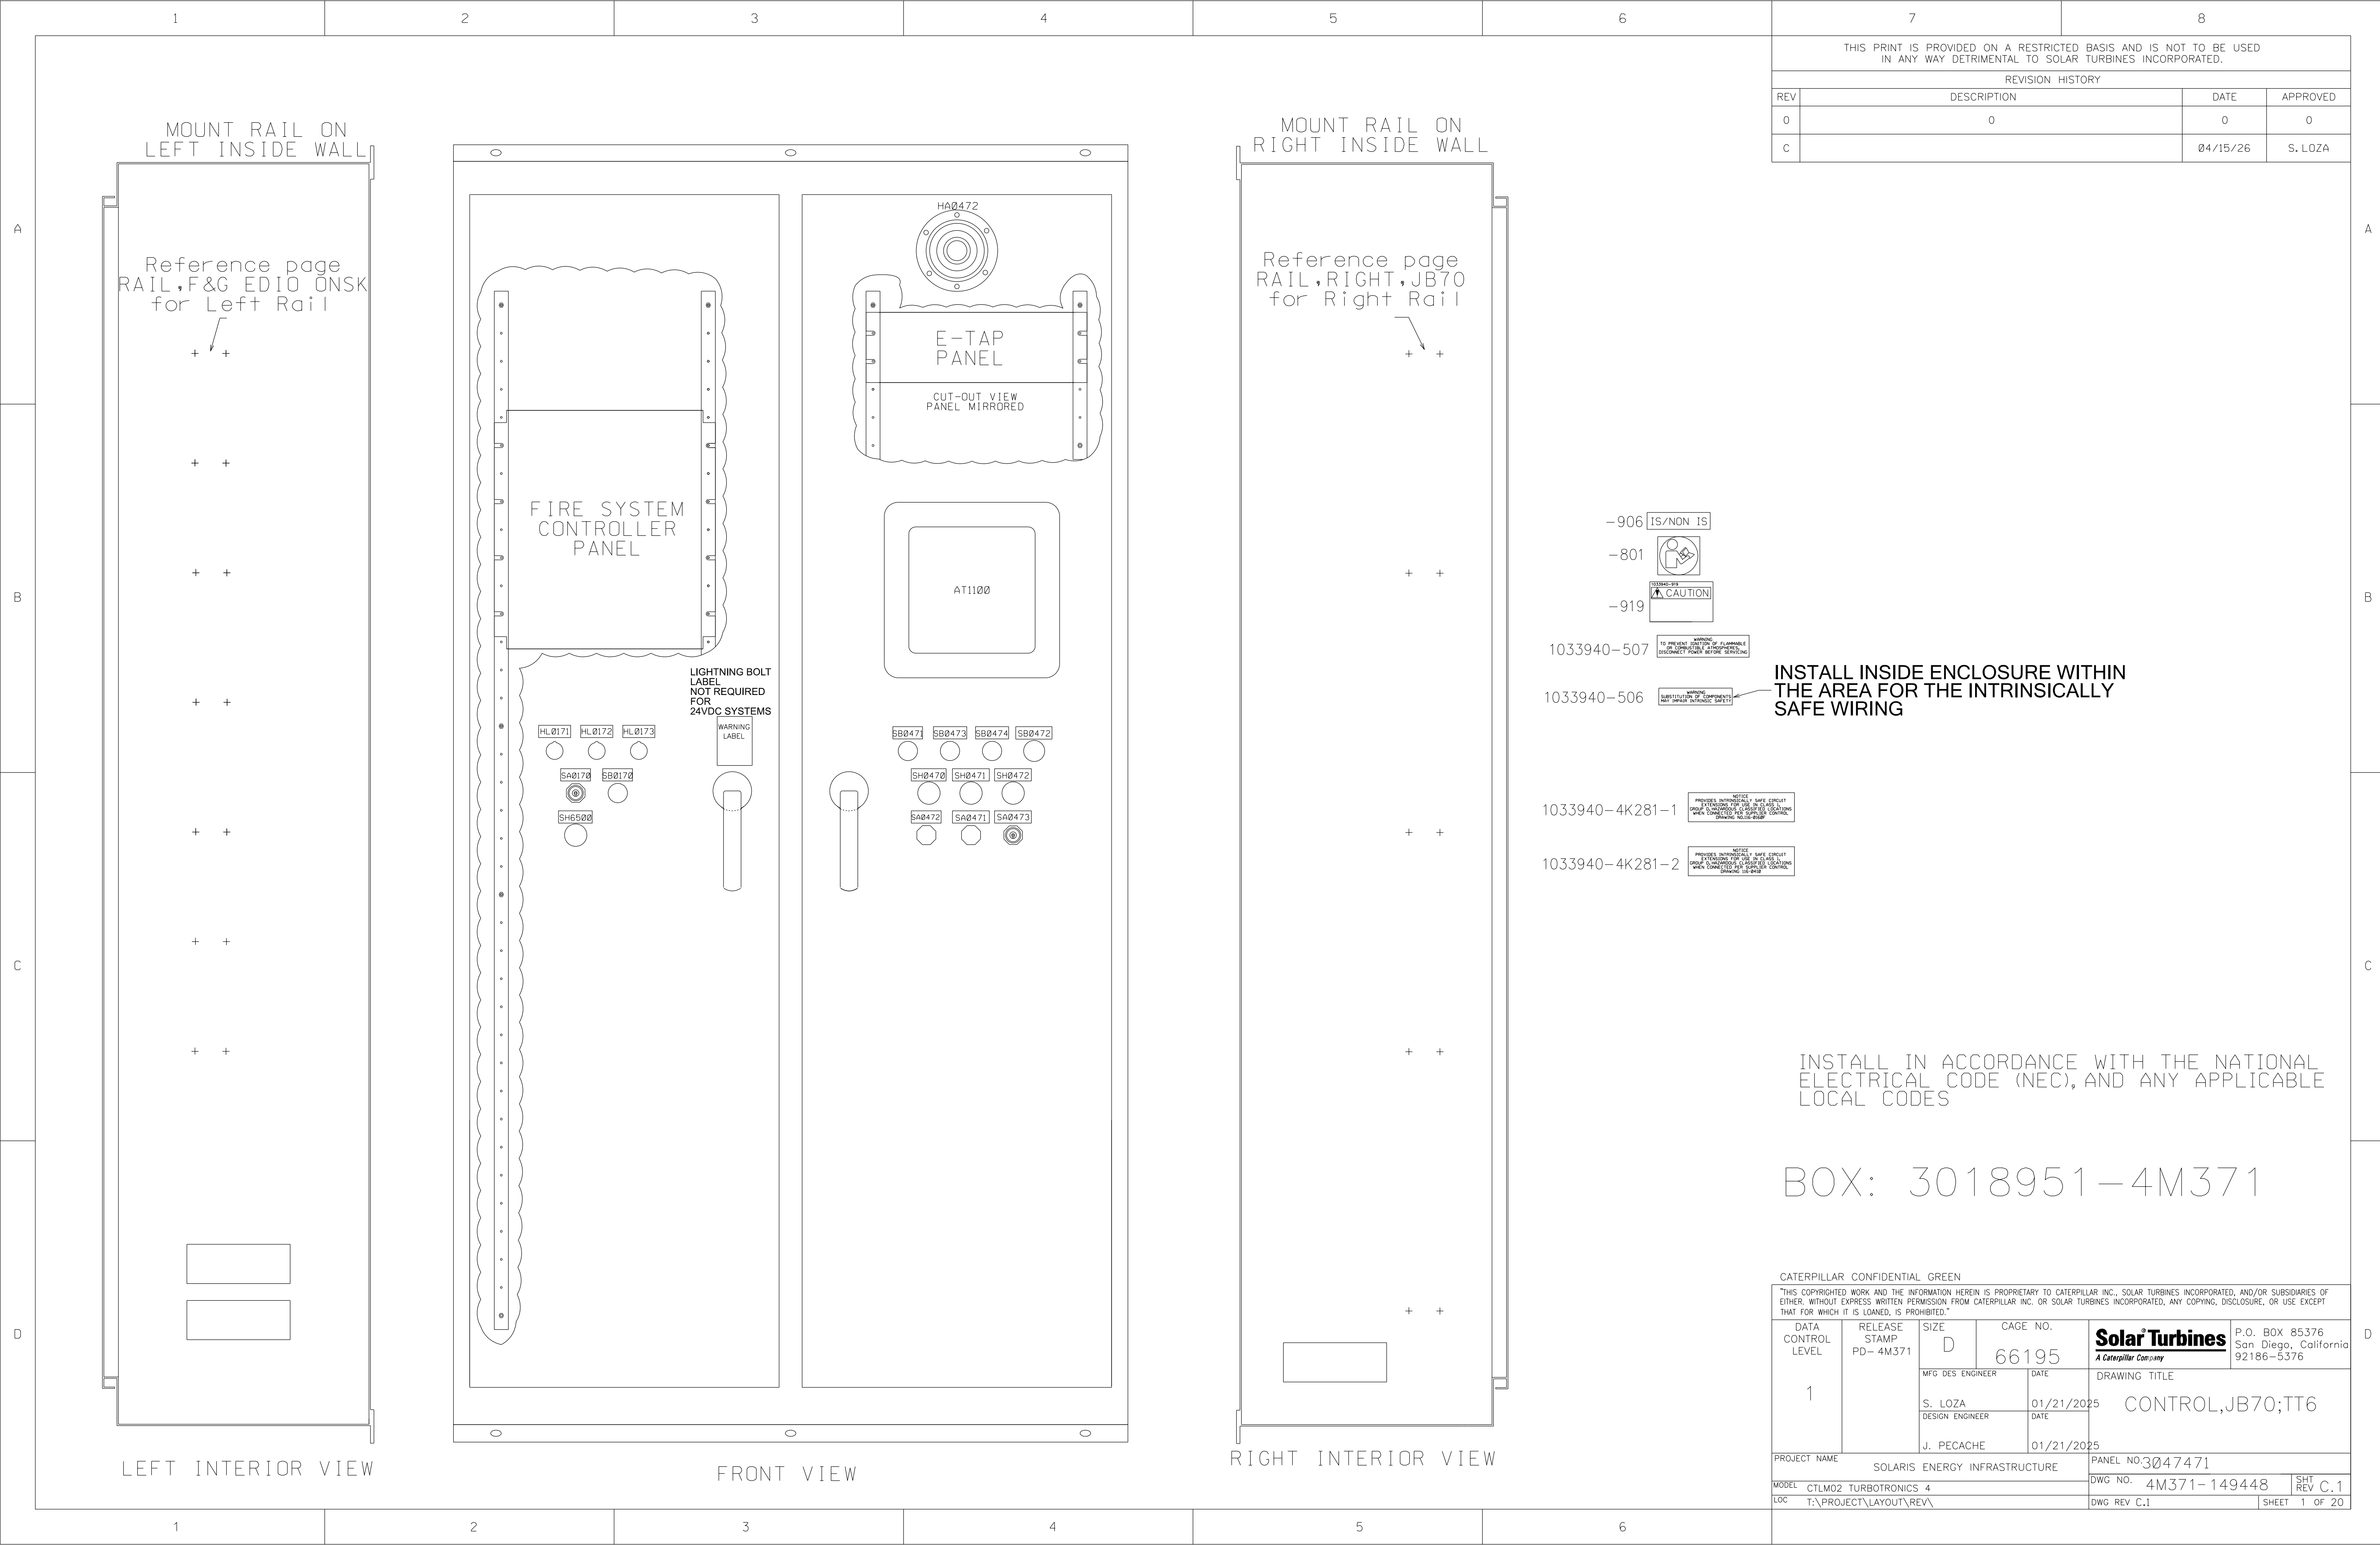

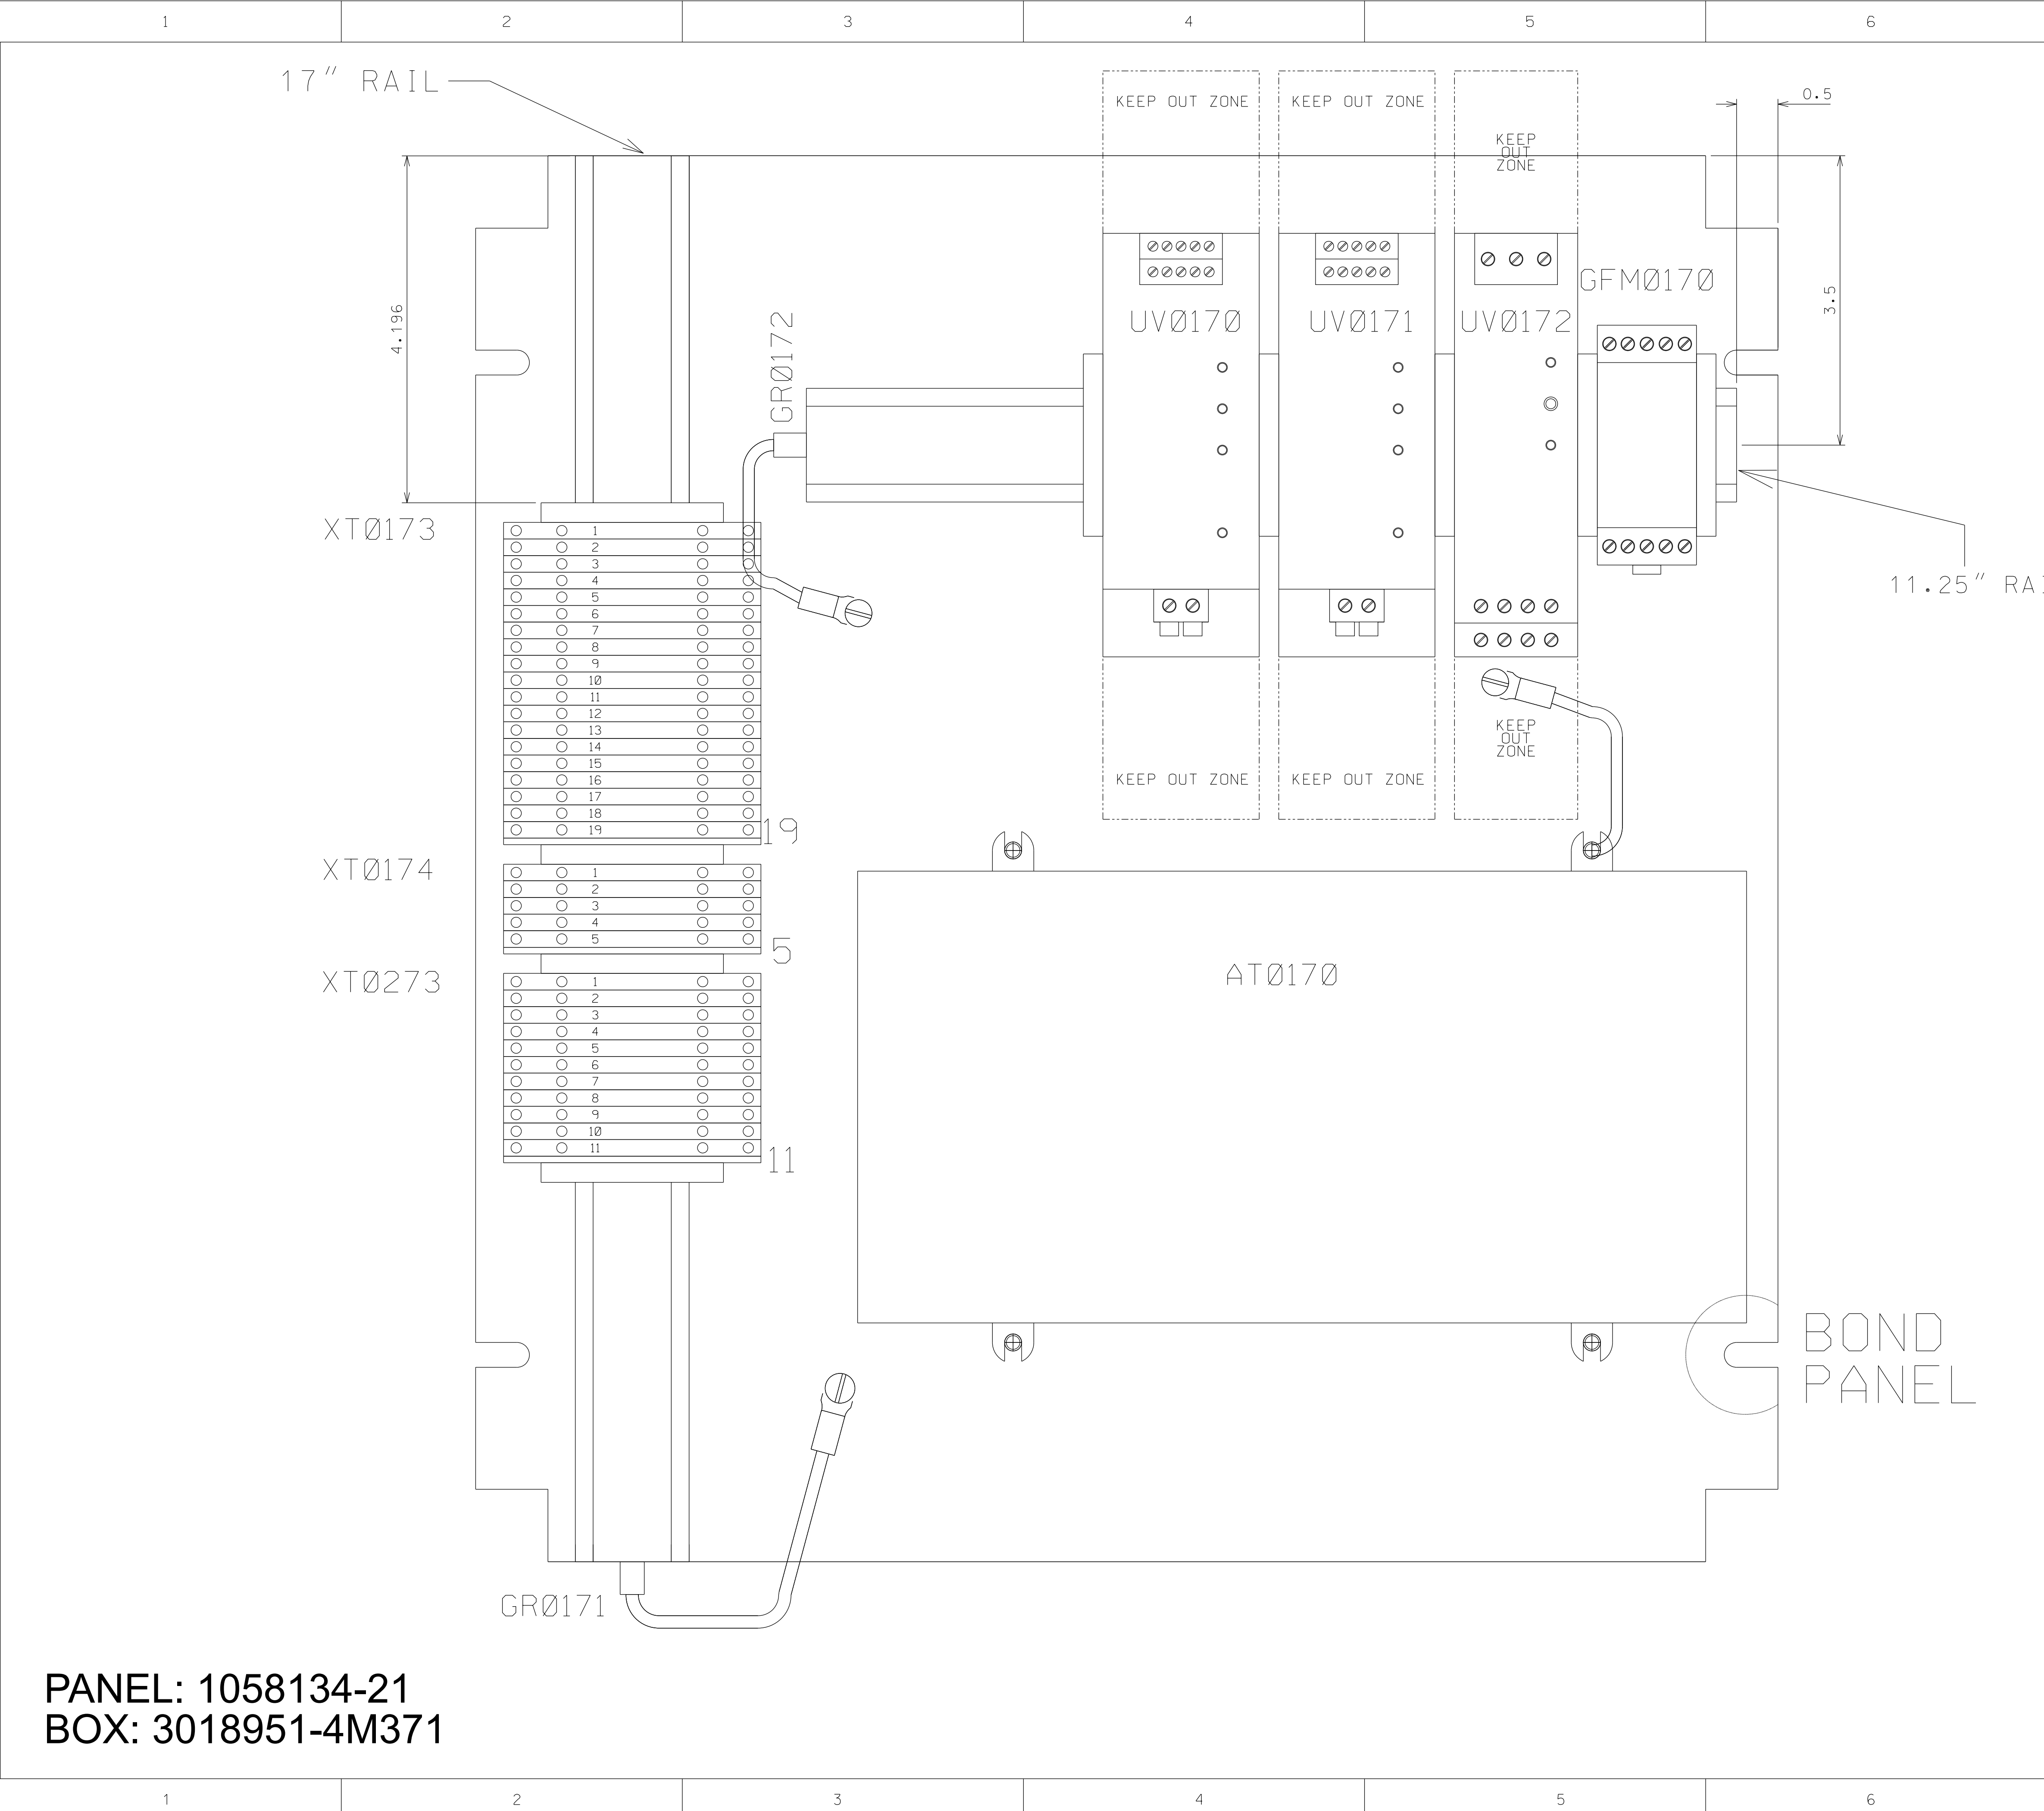

7		8	
THIS PRINT IS PROVIDED ON A RESTRICTED BASIS AND IS NOT TO BE USED IN ANY WAY DETRIMENTAL TO SOLAR TURBINES INCORPORATED.			
REVISION HISTORY			
REV	DESCRIPTION	DATE	APPROVED
0	0	0	0
C		04/15/26	S. LOZA


ADD "GROUND" LABEL TO ALL FG TERMINATION POINTS

INSTALL IN ACCORDANCE WITH THE NATIONAL ELECTRICAL CODE (NEC), AND ANY APPLICABLE LOCAL CODES

PANEL: 1058134-21
BOX: 3018951-4M371

CATERPILLAR CONFIDENTIAL GREEN							
THIS COPYRIGHTED WORK AND THE INFORMATION HEREIN IS PROPRIETARY TO CATERPILLAR INC., SOLAR TURBINES INCORPORATED, AND/OR SUBSIDIARIES OF EITHER. WITHOUT EXPRESS WRITTEN PERMISSION FROM CATERPILLAR INC. OR SOLAR TURBINES INCORPORATED, ANY COPYING, DISCLOSURE, OR USE EXCEPT THAT FOR WHICH IT IS LOANED, IS PROHIBITED.							
DATA CONTROL LEVEL 1	RELEASE STAMP PD- 4M371	SIZE	CAGE NO.		Solar Turbines <i>A Caterpillar Company</i>	P.O. BOX 85376 San Diego, California 92186-5376	
		D	66195				
		MFG DES ENGINEER		DATE			DRAWING TITLE F&G PWR,ONSK
		S. LOZA		01/21/2025			
		DESIGN ENGINEER		DATE			
J. PECACHE		01/21/2025					
PROJECT NAME SOLARIS ENERGY INFRASTRUCTURE					PANEL NO.3005301		
MODEL CTLM02 TURBOTRONICS 4					DWG NO.	4M371- 149448	
LOC T:\PROJECT\LAYOUT\REV\					DWG REV C.1	SHT REV C.1	
					SHEET	4 OF 20	

7		8	
THIS PRINT IS PROVIDED ON A RESTRICTED BASIS AND IS NOT TO BE USED IN ANY WAY DETRIMENTAL TO SOLAR TURBINES INCORPORATED.			
REVISION HISTORY			
REV	DESCRIPTION	DATE	APPROVED
0	0	0	0
C		04/14/26	S. LOZA

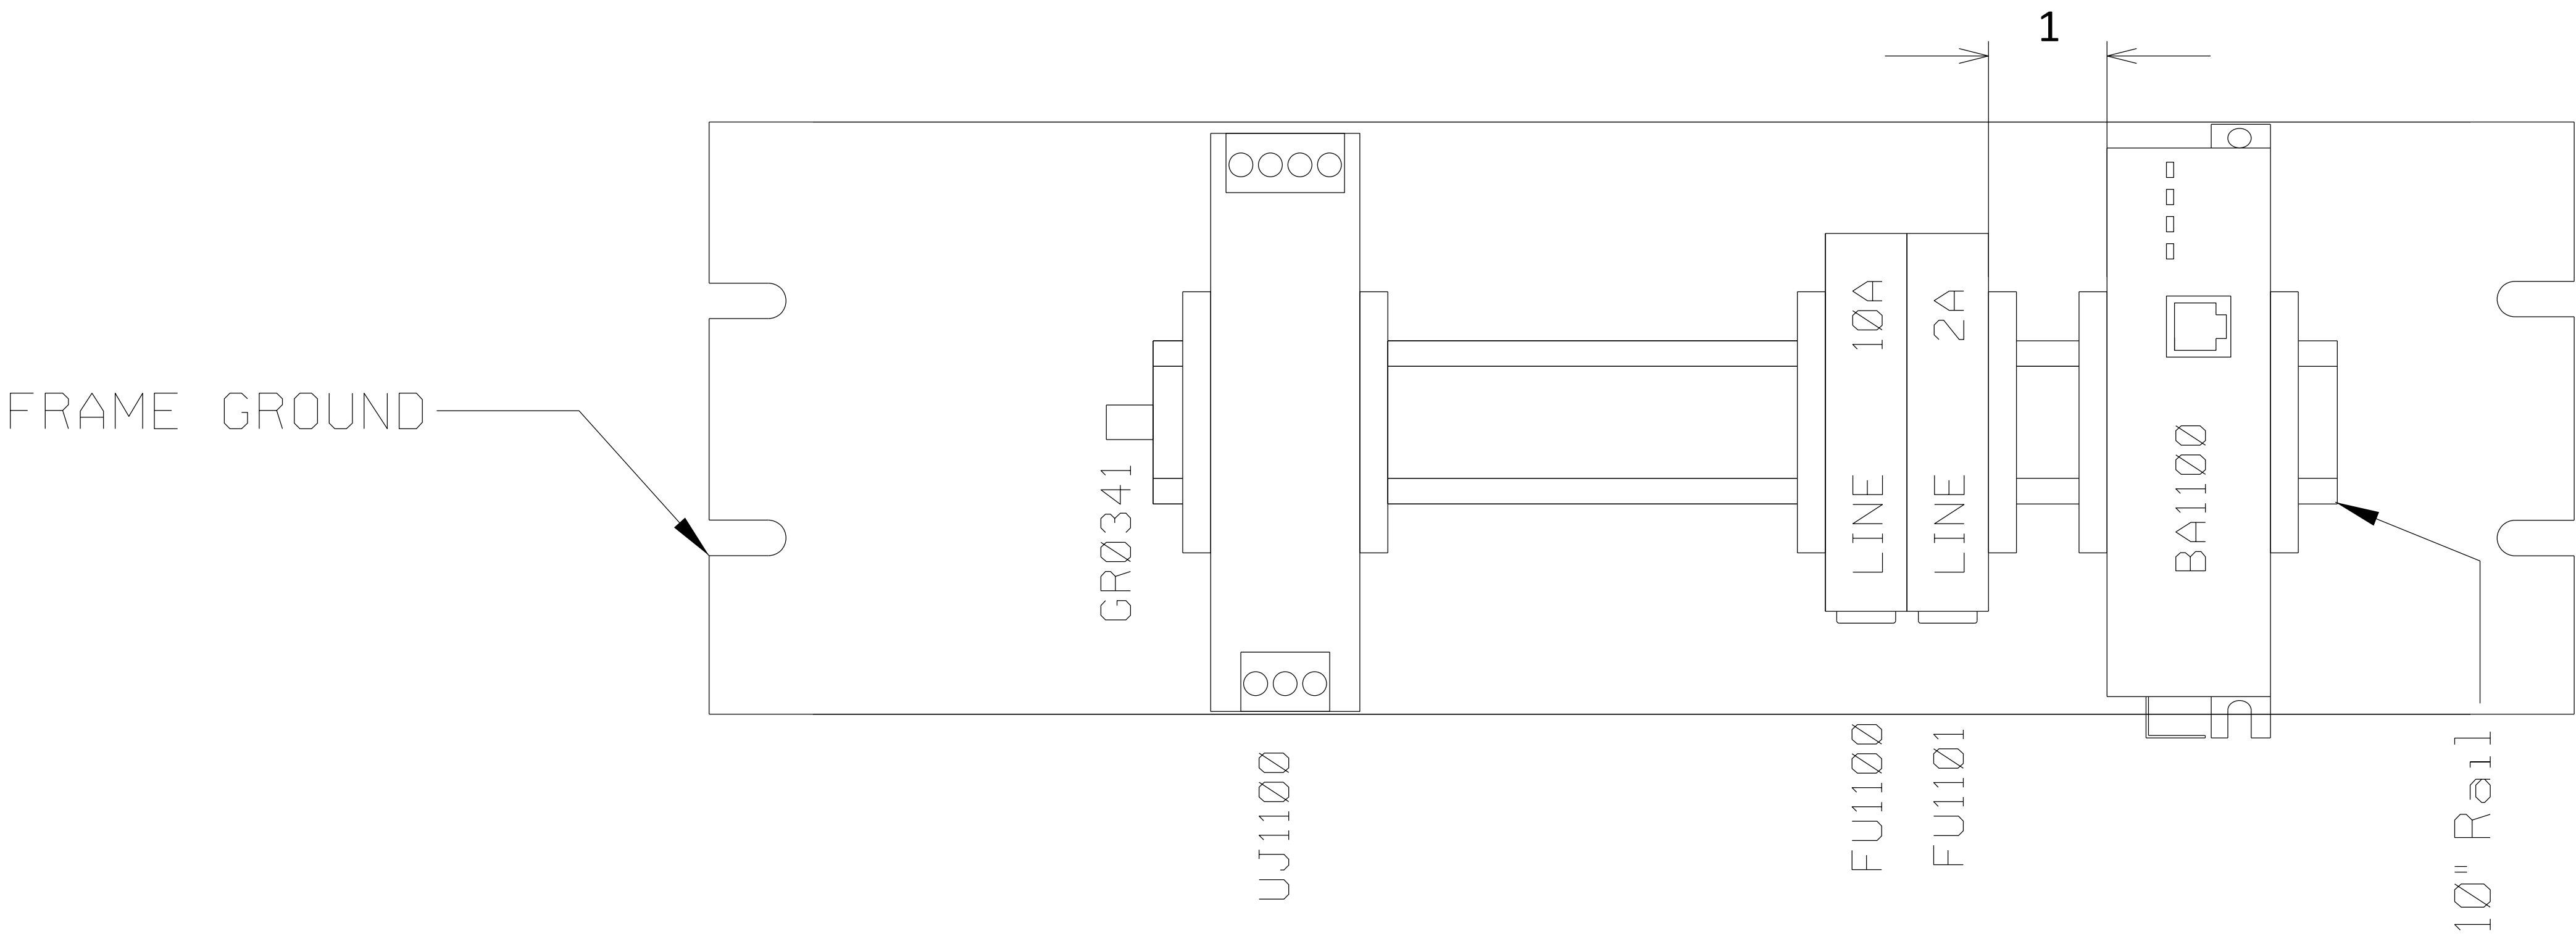


INSTALL IN ACCORDANCE WITH THE NATIONAL ELECTRICAL CODE (NEC), AND ANY APPLICABLE LOCAL CODES

PANEL: 1058134-30
BOX: 3018951-4M371

CATERPILLAR CONFIDENTIAL GREEN						
THIS COPYRIGHTED WORK AND THE INFORMATION HEREIN IS PROPRIETARY TO CATERPILLAR INC., SOLAR TURBINES INCORPORATED, AND/OR SUBSIDIARIES OF EITHER. WITHOUT EXPRESS WRITTEN PERMISSION FROM CATERPILLAR INC. OR SOLAR TURBINES INCORPORATED, ANY COPYING, DISCLOSURE, OR USE EXCEPT THAT FOR WHICH IT IS LOANED, IS PROHIBITED.						
DATA CONTROL LEVEL 1	RELEASE STAMP PD- 4M371	SIZE D	CAGE NO. 66195		Solar Turbines <i>A Caterpillar Company</i>	P.O. BOX 85376 San Diego, California 92186-5376
		MFG DES ENGINEER	DATE	DRAWING TITLE HMI-S PWR,JB70		
		S. LOZA	01/21/2025			
		DESIGN ENGINEER	DATE			
		J. PECACHE	01/21/2025			
PROJECT NAME SOLARIS ENERGY INFRASTRUCTURE				PANEL NO.3067767		
MODEL	CTLM02 TURBOTRONICS 4			DWG NO.	4M371-149448	SHT REV C
LOC	T:\PROJECT\LAYOUT\REV\			DWG REV C.1	SHEET 5 OF 20	


7		8	
THIS PRINT IS PROVIDED ON A RESTRICTED BASIS AND IS NOT TO BE USED IN ANY WAY DETRIMENTAL TO SOLAR TURBINES INCORPORATED.			
REVISION HISTORY			
REV	DESCRIPTION	DATE	APPROVED
0	0	0	0
C		04/14/26	S. LOZA

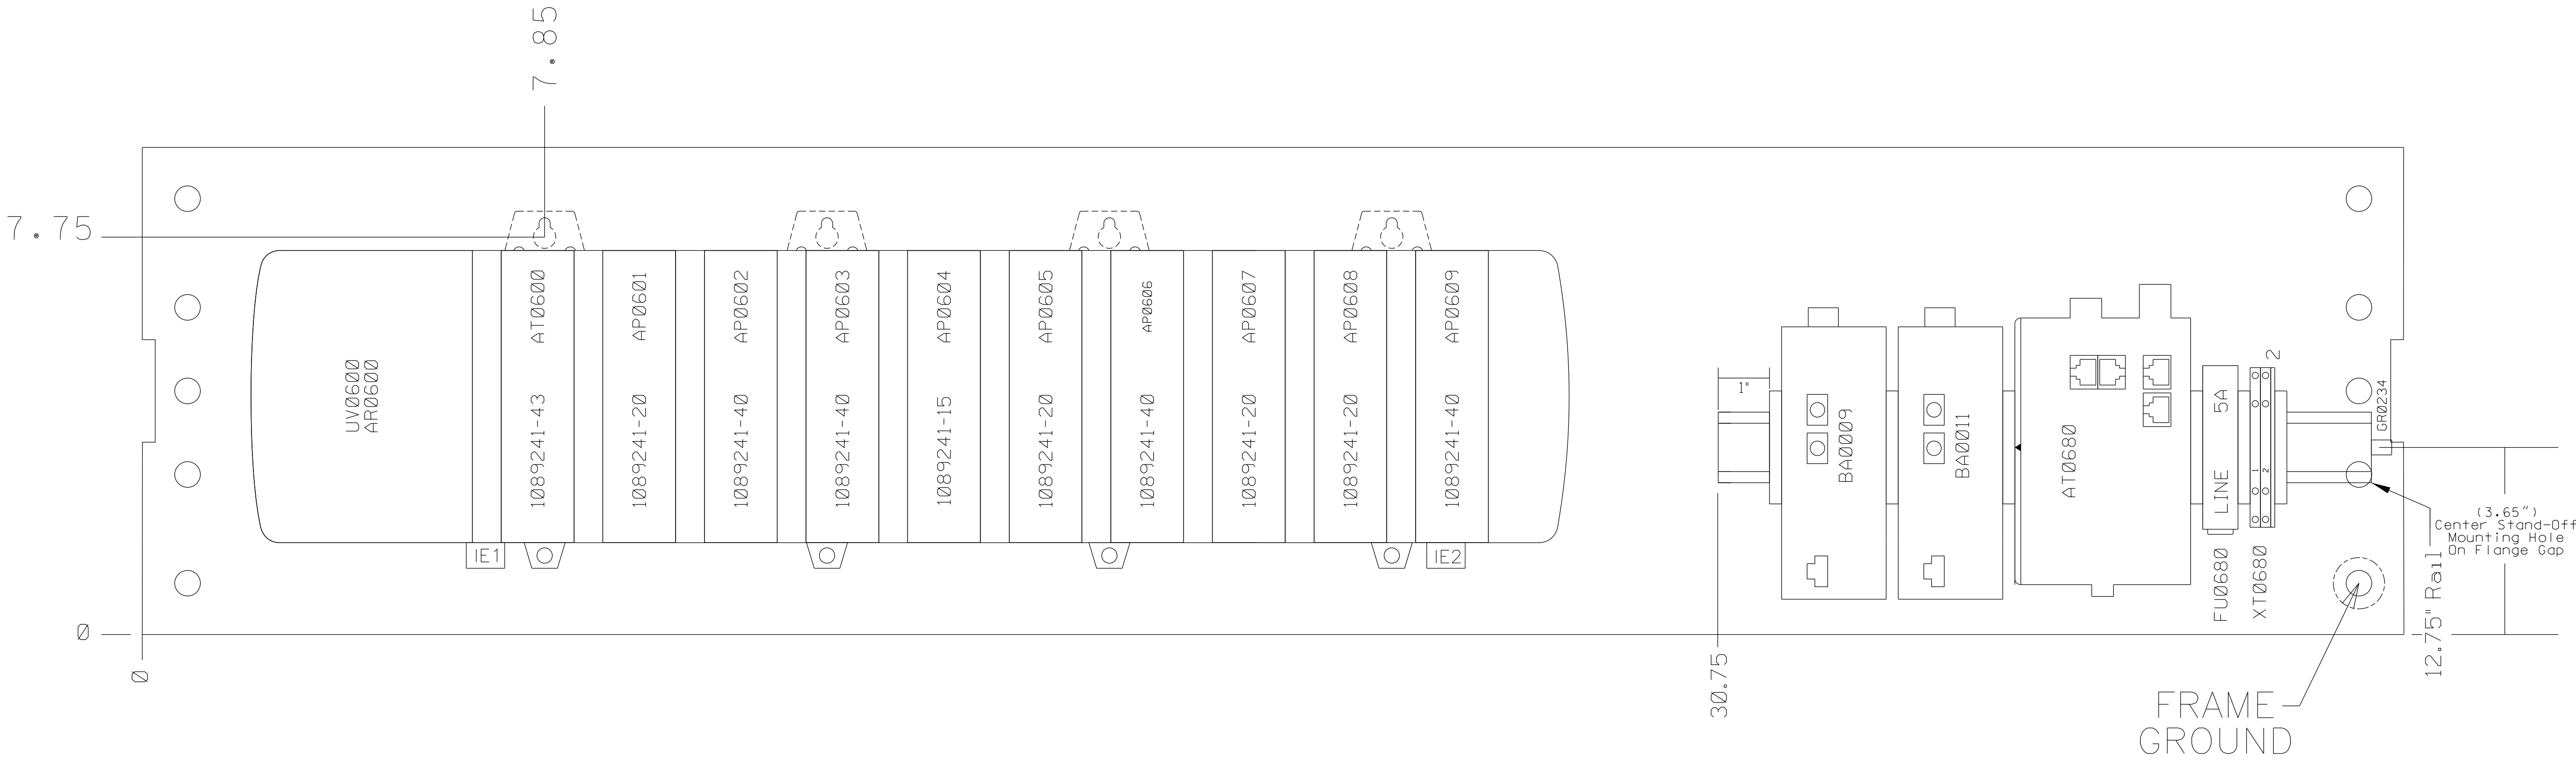


INSTALL IN ACCORDANCE WITH THE NATIONAL ELECTRICAL CODE (NEC), AND ANY APPLICABLE LOCAL CODES

PANEL: 1053331-1600
BOX: 3018951-4M371

CATERPILLAR CONFIDENTIAL GREEN						
THIS COPYRIGHTED WORK AND THE INFORMATION HEREIN IS PROPRIETARY TO CATERPILLAR INC., SOLAR TURBINES INCORPORATED, AND/OR SUBSIDIARIES OF EITHER. WITHOUT EXPRESS WRITTEN PERMISSION FROM CATERPILLAR INC. OR SOLAR TURBINES INCORPORATED, ANY COPYING, DISCLOSURE, OR USE EXCEPT THAT FOR WHICH IT IS LOANED, IS PROHIBITED.						
DATA CONTROL LEVEL 1	RELEASE STAMP PD- 4M371	SIZE	CAGE NO.		Solar Turbines <i>A Caterpillar Company</i>	P.O. BOX 85376 San Diego, California 92186-5376
		D	66195			
		MFG DES ENGINEER	DATE	DRAWING TITLE		
		S. LOZA	01/21/2025			
		DESIGN ENGINEER	DATE			
J. PECACHE	01/21/2025	PLC				
PROJECT NAME					PANEL NO.3006021	
SOLARIS ENERGY INFRASTRUCTURE						
MODEL	CTLMO2 TURBOTRONICS 4				DWG NO.	4M371-149448
LOC	T:\PROJECT\LAYOUT\REV\				DWG REV C.1	SHT REV C
					SHEET	6 OF 20

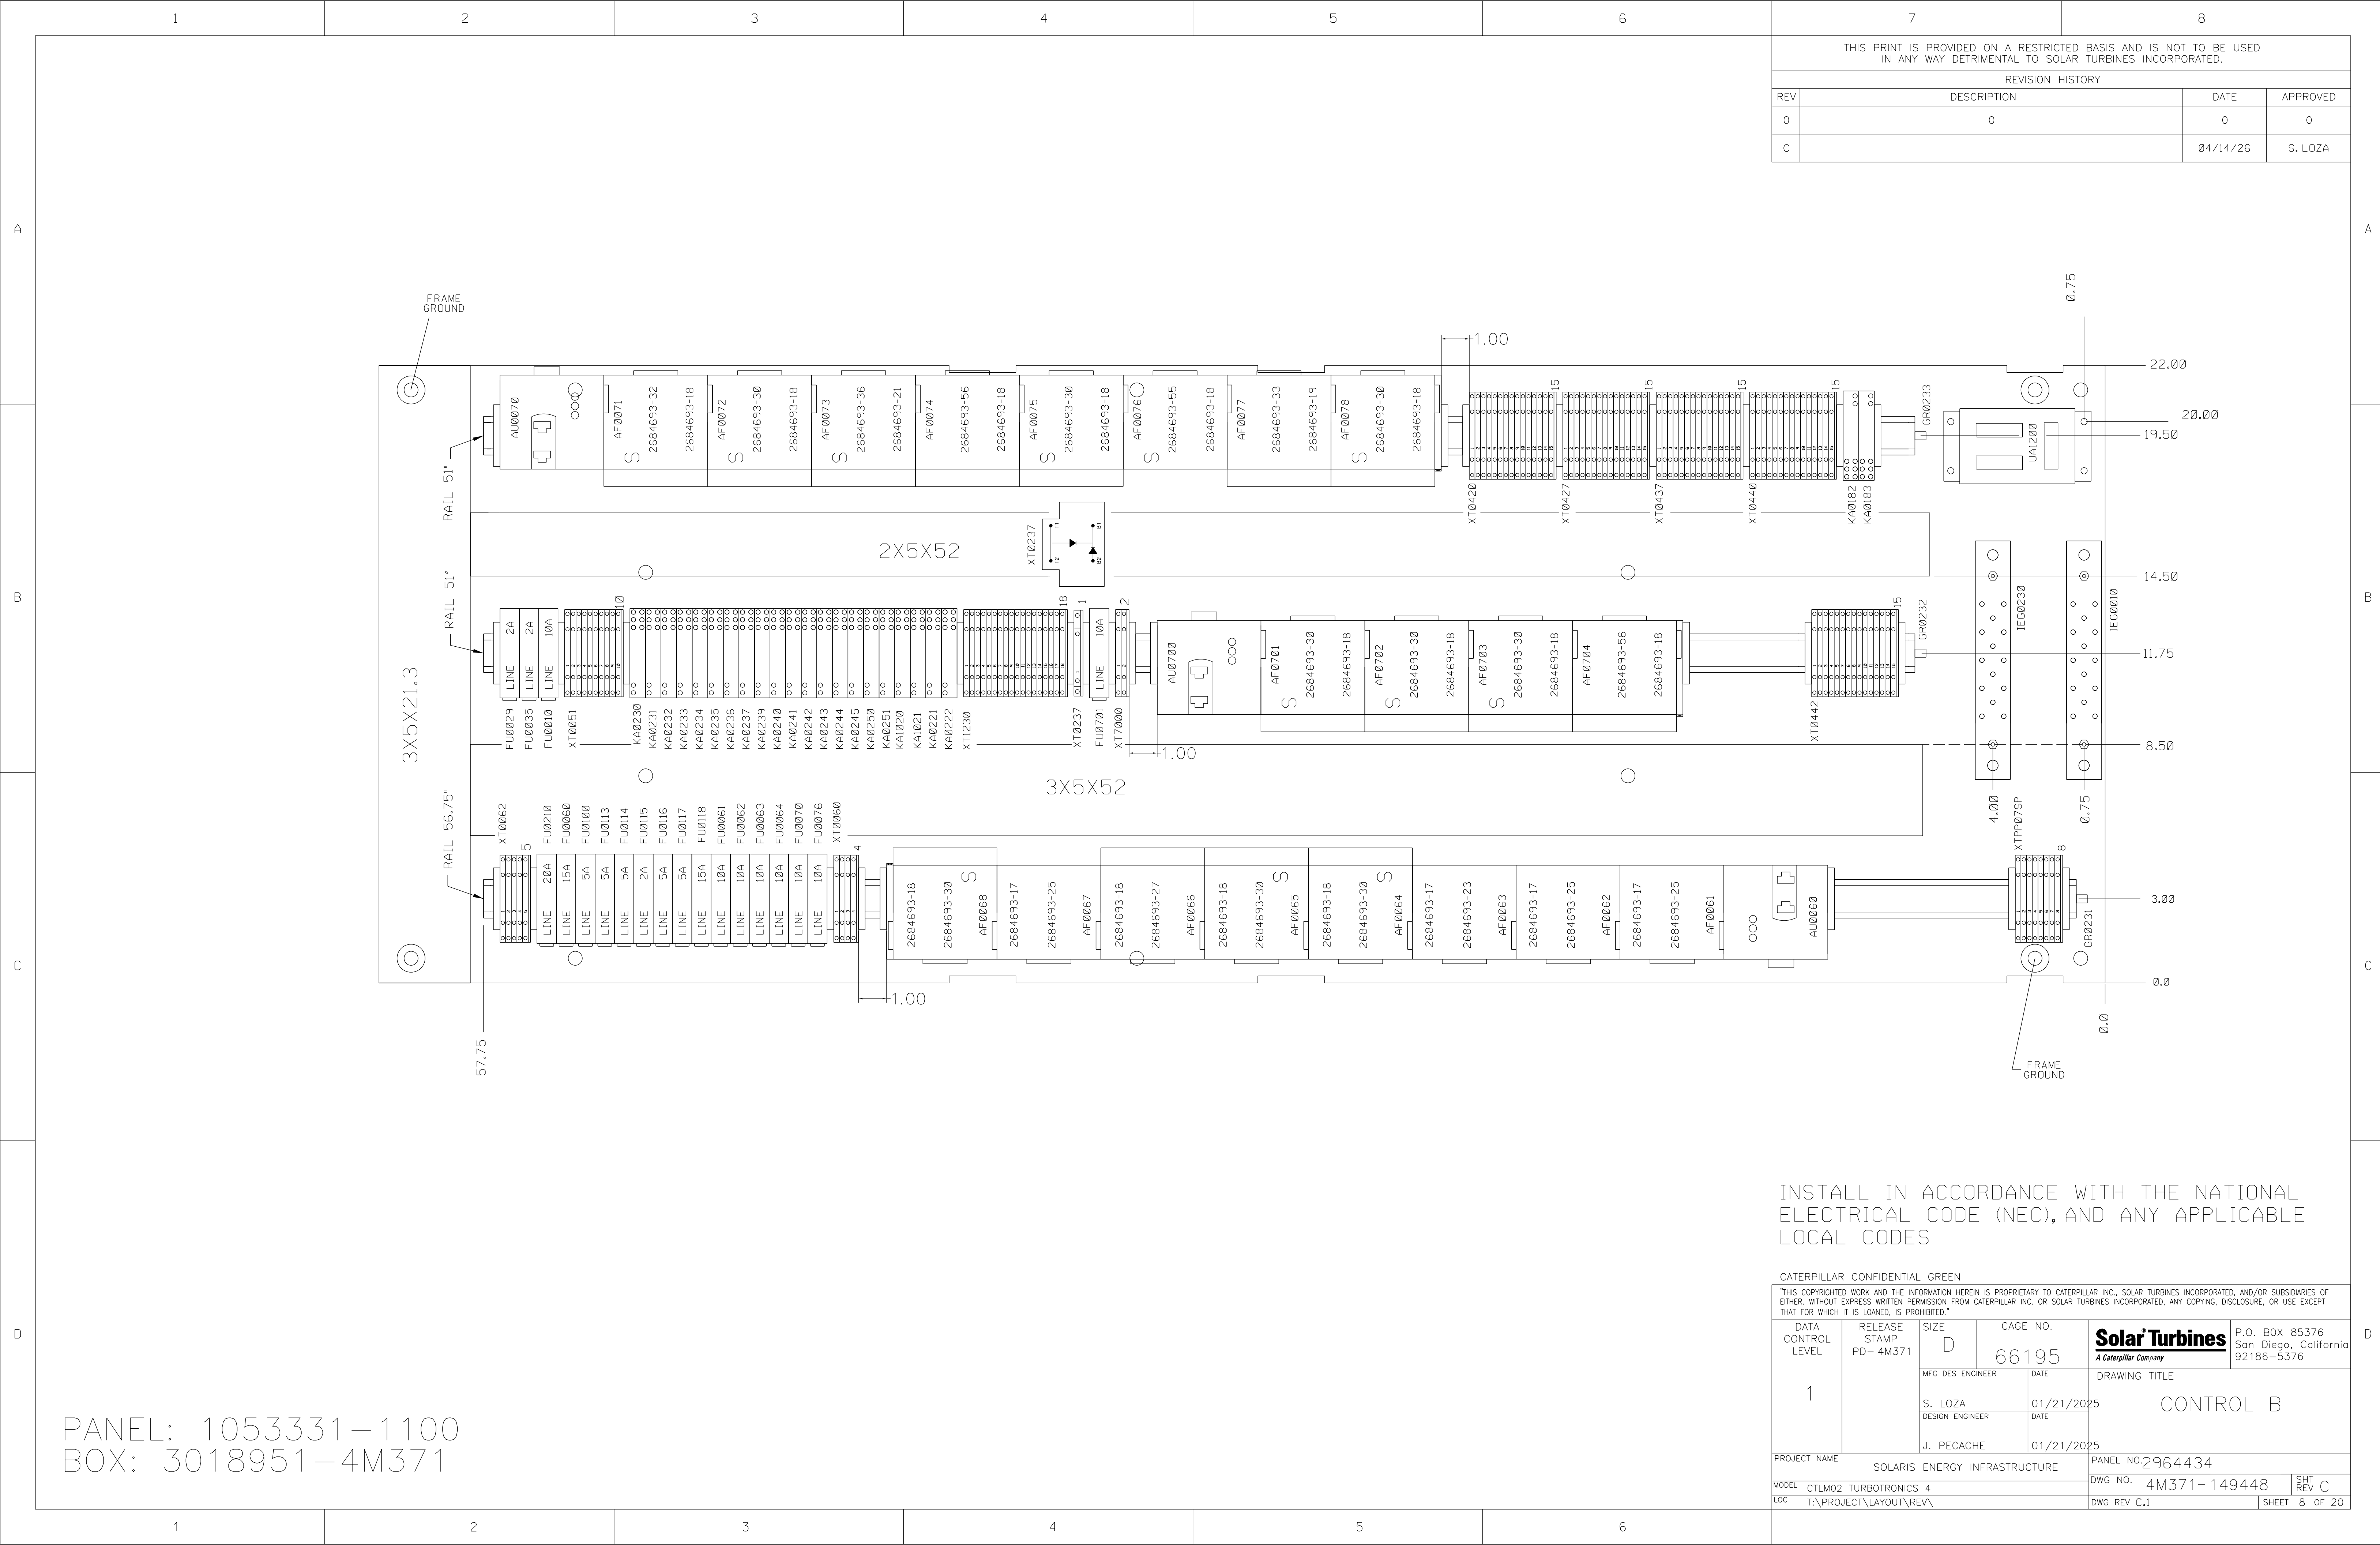

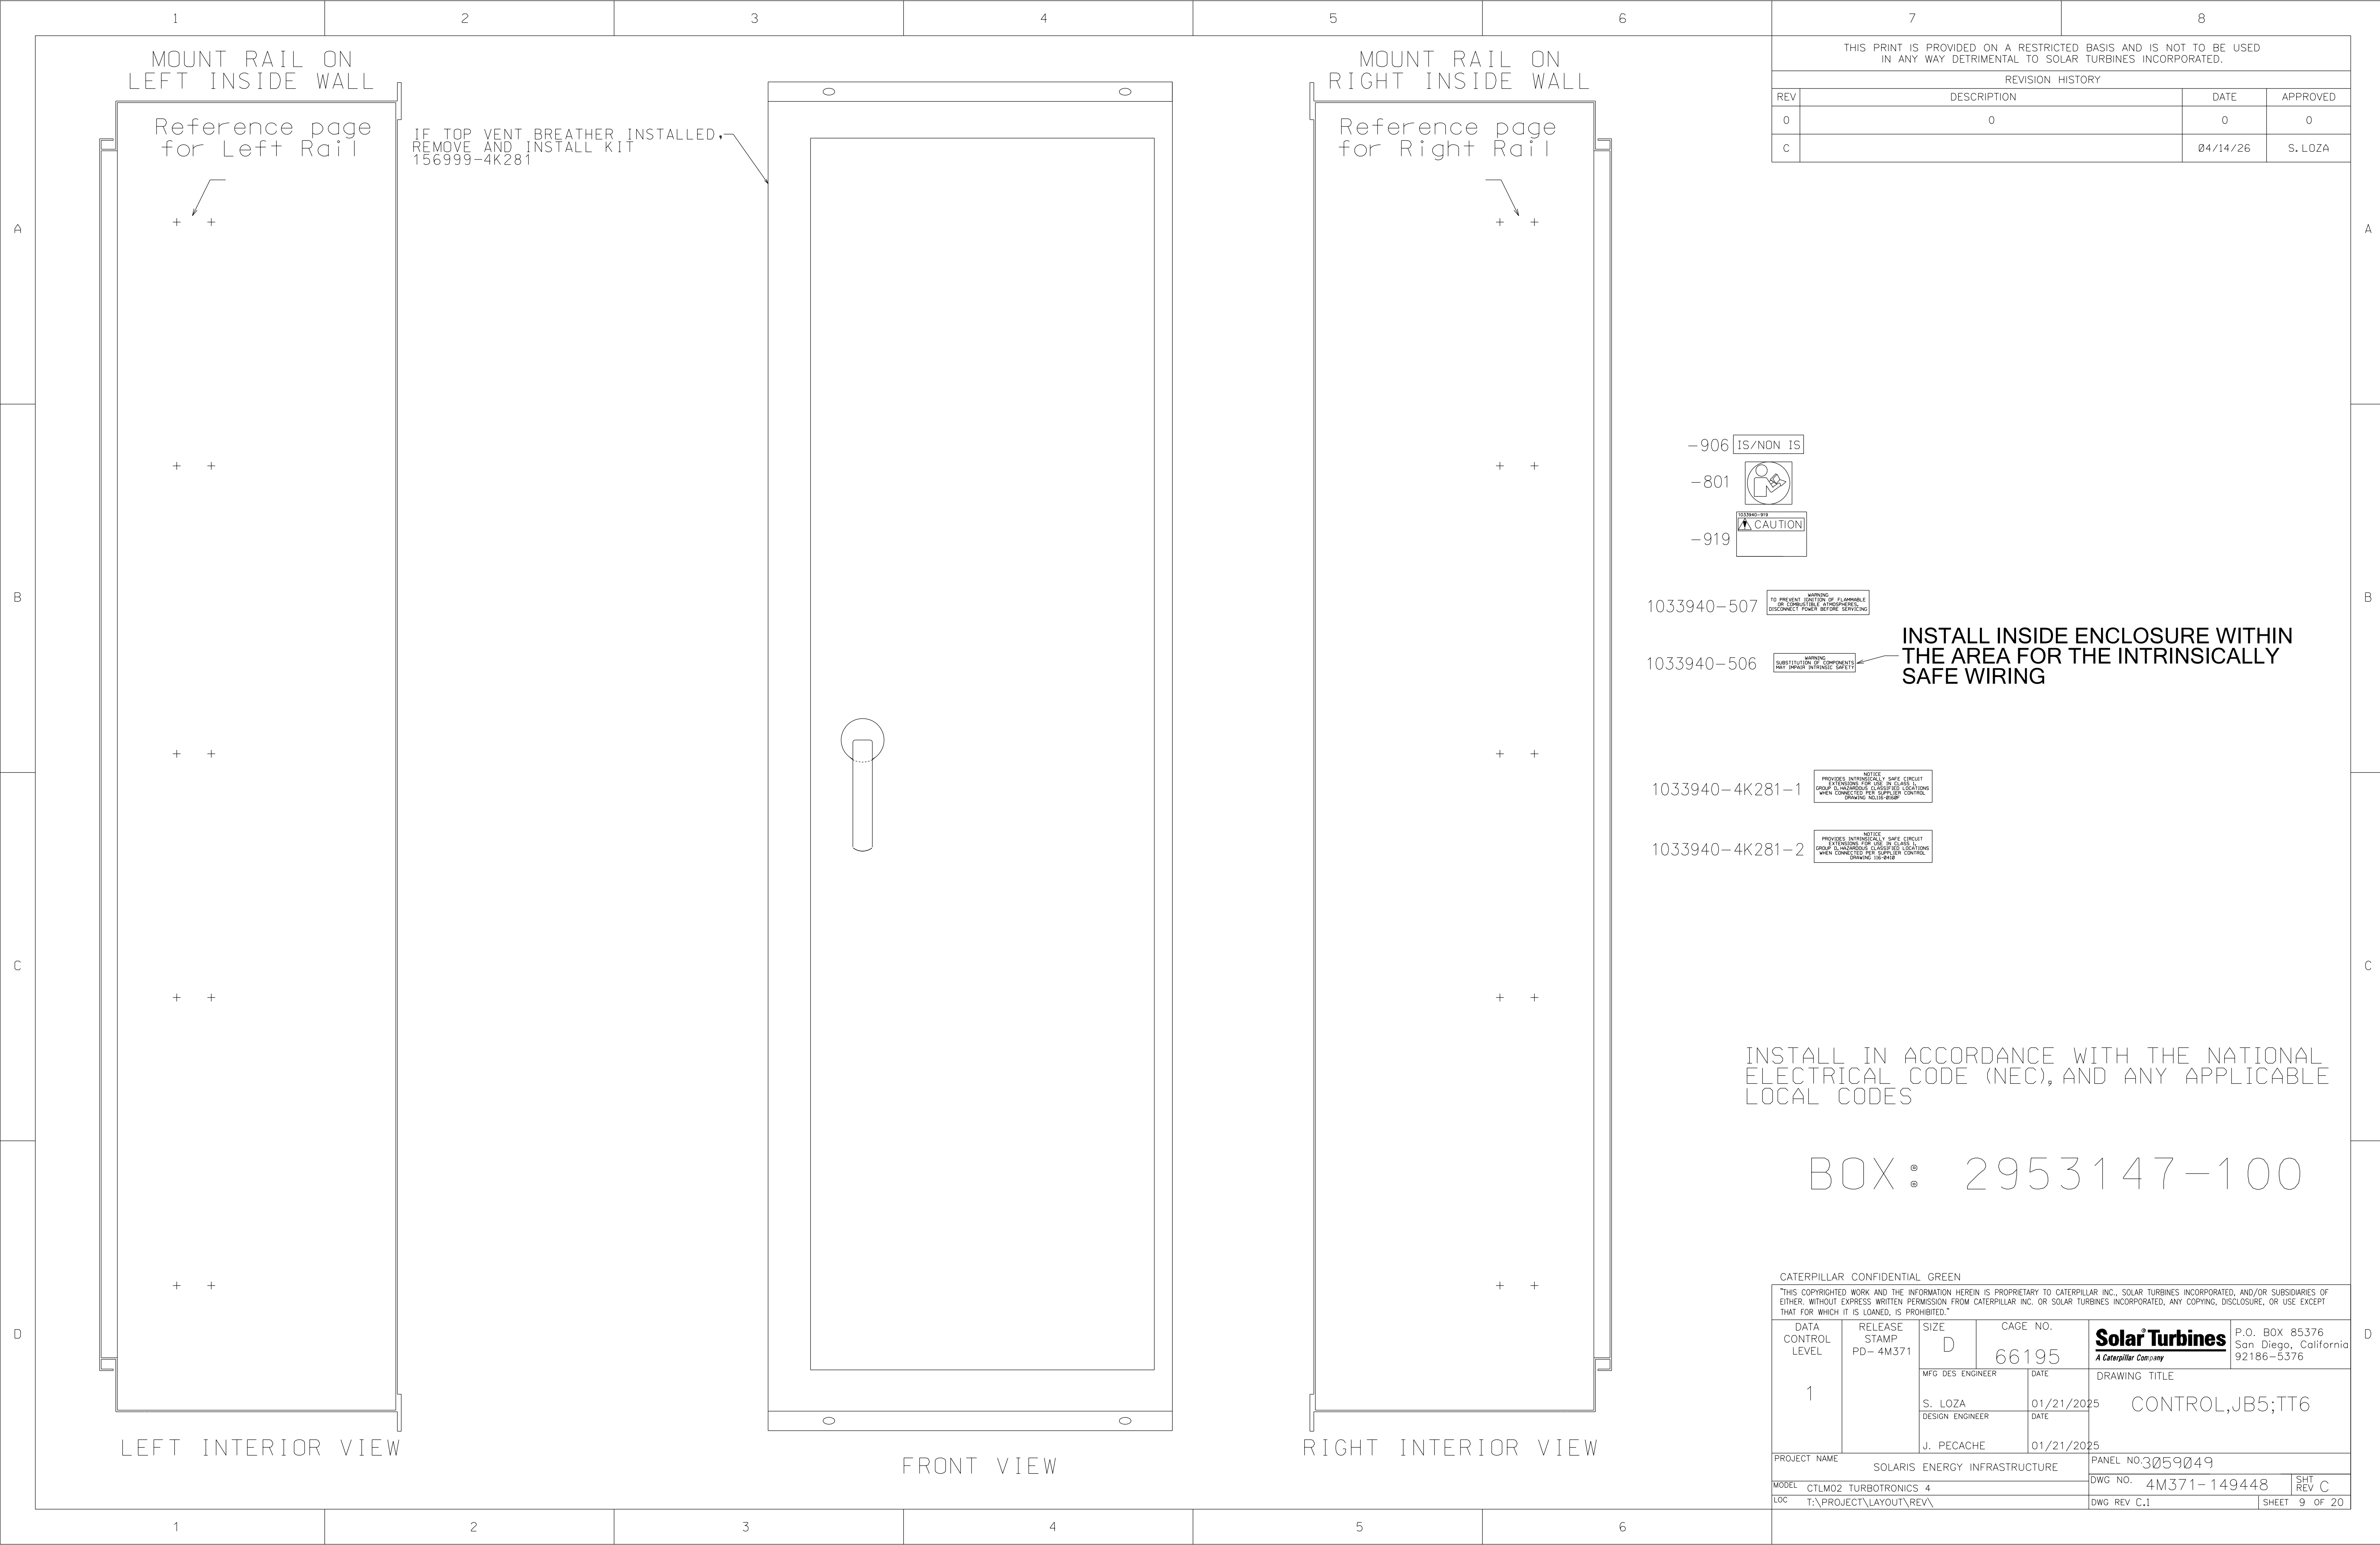

7		8	
THIS PRINT IS PROVIDED ON A RESTRICTED BASIS AND IS NOT TO BE USED IN ANY WAY DETRIMENTAL TO SOLAR TURBINES INCORPORATED.			
REVISION HISTORY			
REV	DESCRIPTION	DATE	APPROVED
0	0	0	0
C		04/14/26	S. LOZA

ADD "GROUND" LABEL TO ALL
FG TERMINATION POINTS



SEE THE CONTROL DRAWING FOR EACH INTRINSIC
SAFETY BARRIER FOR PERMITTED CONNECTIONS
AND IDENTIFICATION OF THE ELECTRICAL (ENTITY)
PARAMETERS OF EACH BARRIER, ALONG WITH
OTHER INFORMATION FOR SAFE INTERCONNECTION


INSTALL IN ACCORDANCE WITH THE NATIONAL
ELECTRICAL CODE (NEC), AND ANY APPLICABLE
LOCAL CODES

BOX : 2953147-100

CATERPILLAR CONFIDENTIAL GREEN					
"THIS COPYRIGHTED WORK AND THE INFORMATION HEREIN IS PROPRIETARY TO CATERPILLAR INC., SOLAR TURBINES INCORPORATED, AND/OR SUBSIDIARIES OF EITHER. WITHOUT EXPRESS WRITTEN PERMISSION FROM CATERPILLAR INC. OR SOLAR TURBINES INCORPORATED, ANY COPYING, DISCLOSURE, OR USE EXCEPT THAT FOR WHICH IT IS LOANED, IS PROHIBITED."					
DATA CONTROL LEVEL 1	RELEASE STAMP PD- 4M371	SIZE D	CAGE NO. 66195		Solar[®]Turbines <i>A Caterpillar Company</i> P.O. BOX 85376 San Diego, California 92186-5376
		MFG DES ENGINEER	DATE	DRAWING TITLE RAIL,RIGHT,JB5	
		S. LOZA DESIGN ENGINEER	01/21/2025		
		J. PECACHE	01/21/2025		
PROJECT NAME SOLARIS ENERGY INFRASTRUCTURE				PANEL NO.2967178	
MODEL	CTLMO2 TURBOTRONICS 4			DWG NO.	4M371- 149448
LOC	T:\PROJECT\LAYOUT\REV\			DWG REV C.1	SHT REV C
				SHEET	11 OF 20

7		8	
THIS PRINT IS PROVIDED ON A RESTRICTED BASIS AND IS NOT TO BE USED IN ANY WAY DETRIMENTAL TO SOLAR TURBINES INCORPORATED.			
REVISION HISTORY			
REV	DESCRIPTION	DATE	APPROVED
0	0	0	0
C		04/14/26	S. LOZA

ADD "GROUND" LABEL TO ALL
FG TERMINATION POINTS

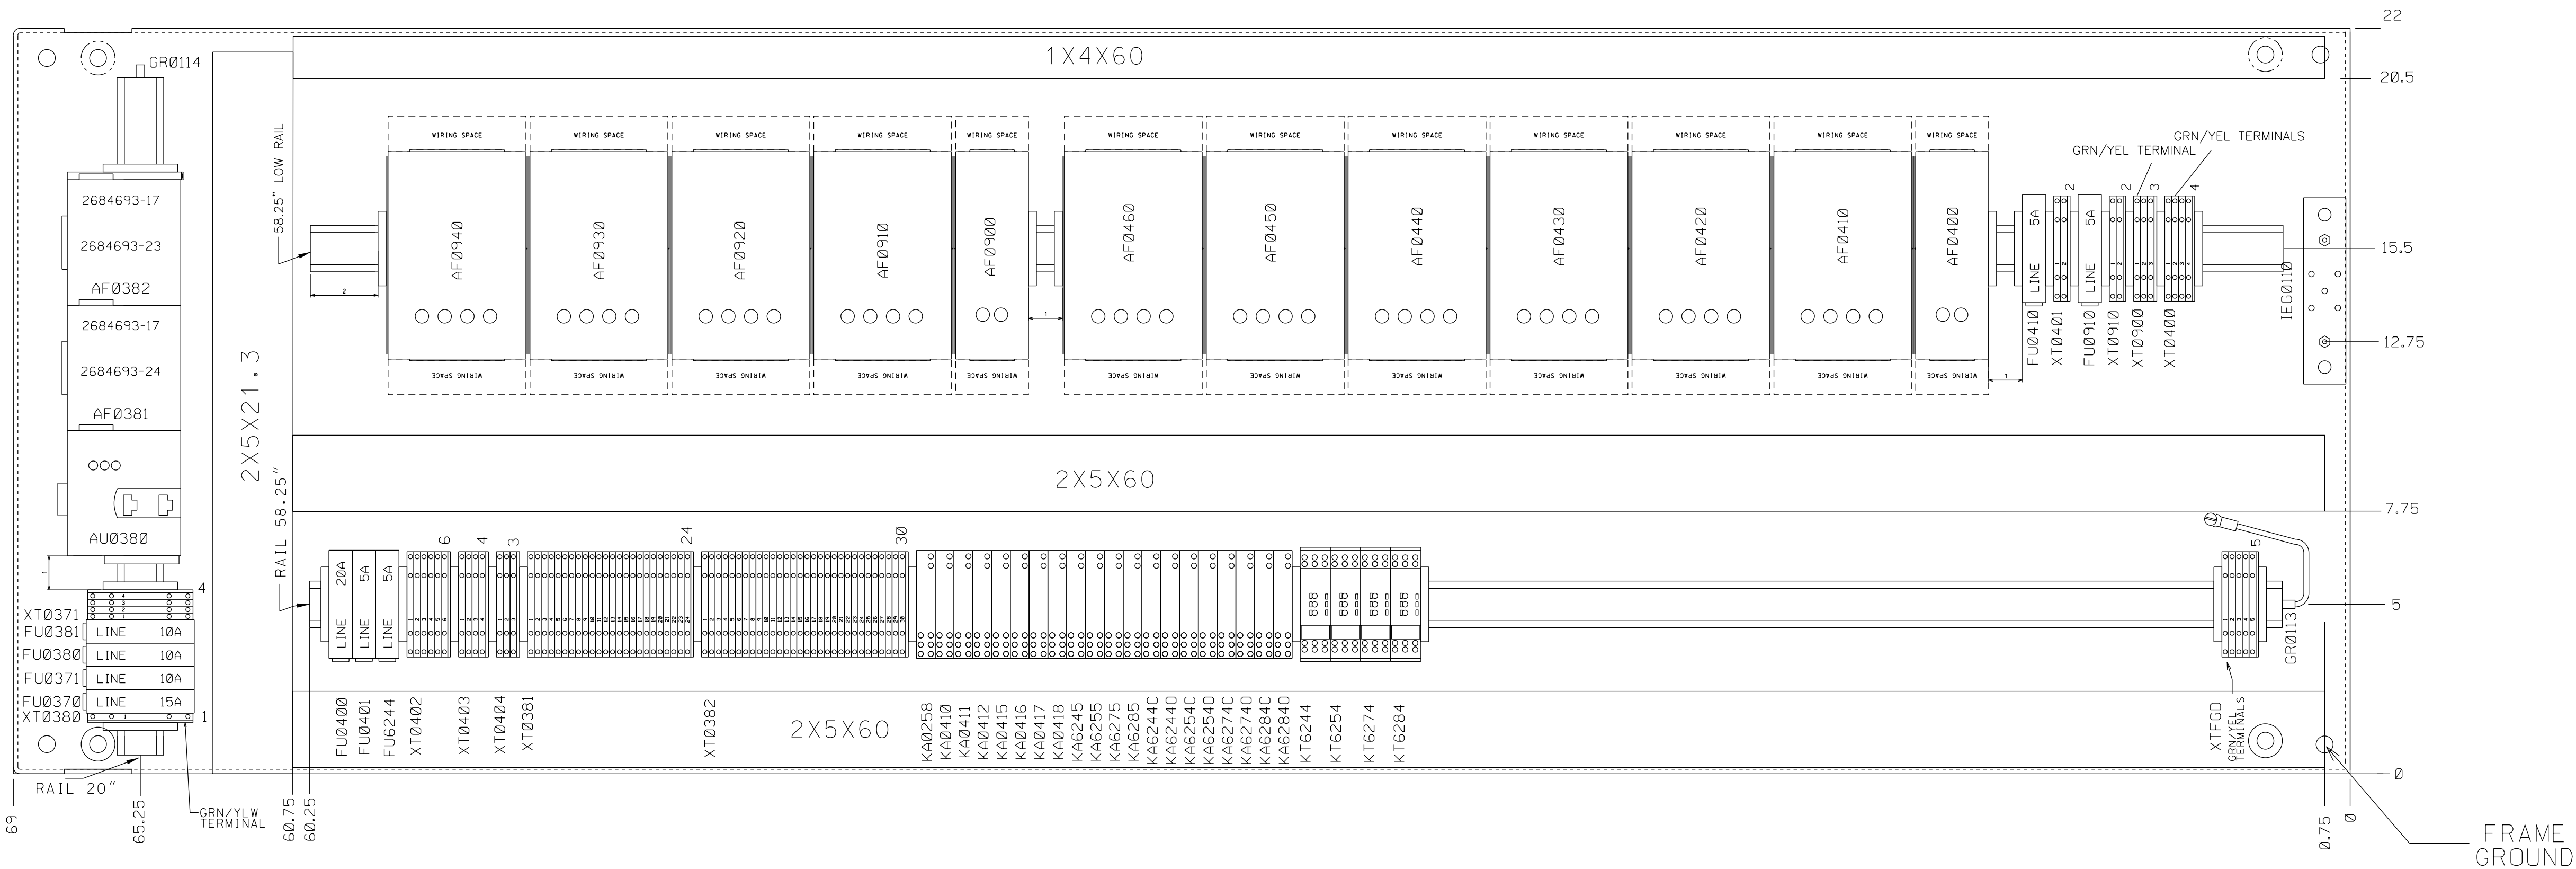

INSTALL IN ACCORDANCE WITH THE NATIONAL
ELECTRICAL CODE (NEC), AND ANY APPLICABLE
LOCAL CODES

PANEL : 1053331-501
BOX : 2953147-100

CATERPILLAR CONFIDENTIAL GREEN					
"THIS COPYRIGHTED WORK AND THE INFORMATION HEREIN IS PROPRIETARY TO CATERPILLAR INC., SOLAR TURBINES INCORPORATED, AND/OR SUBSIDIARIES OF EITHER. WITHOUT EXPRESS WRITTEN PERMISSION FROM CATERPILLAR INC. OR SOLAR TURBINES INCORPORATED, ANY COPYING, DISCLOSURE, OR USE EXCEPT THAT FOR WHICH IT IS LOANED, IS PROHIBITED."					
DATA CONTROL LEVEL	RELEASE STAMP PD- 4M371	SIZE	CAGE NO.	Solar Turbines <i>A Caterpillar Company</i>	P.O. BOX 85376 San Diego, California 92186-5376
		D	66195		
		MFG DES ENGINEER	DATE		
		S. LOZA	01/21/2025		
1		DESIGN ENGINEER	DATE	DRAWING TITLE	TURBINE VIBRATION JB5
		J. PECACHE	01/21/2025		
PROJECT NAME				SOLARIS ENERGY INFRASTRUCTURE	
				PANEL NO.2970436	
MODEL	CTLMO2 TURBOTRONICS 4			DWG NO. 4M371-149448	SHT REV C
LOC	T:\PROJECT\LAYOUT\REV\			DWG REV C.1	SHEET 12 OF 20

1

2

3

4

5

6


7

8

MOUNT RAIL ON
LEFT INSIDE WALL

MOUNT RAIL ON
RIGHT INSIDE WALL

IF TOP VENT BREATHER INSTALLED,
REMOVE AND INSTALL KIT
156999-4K281

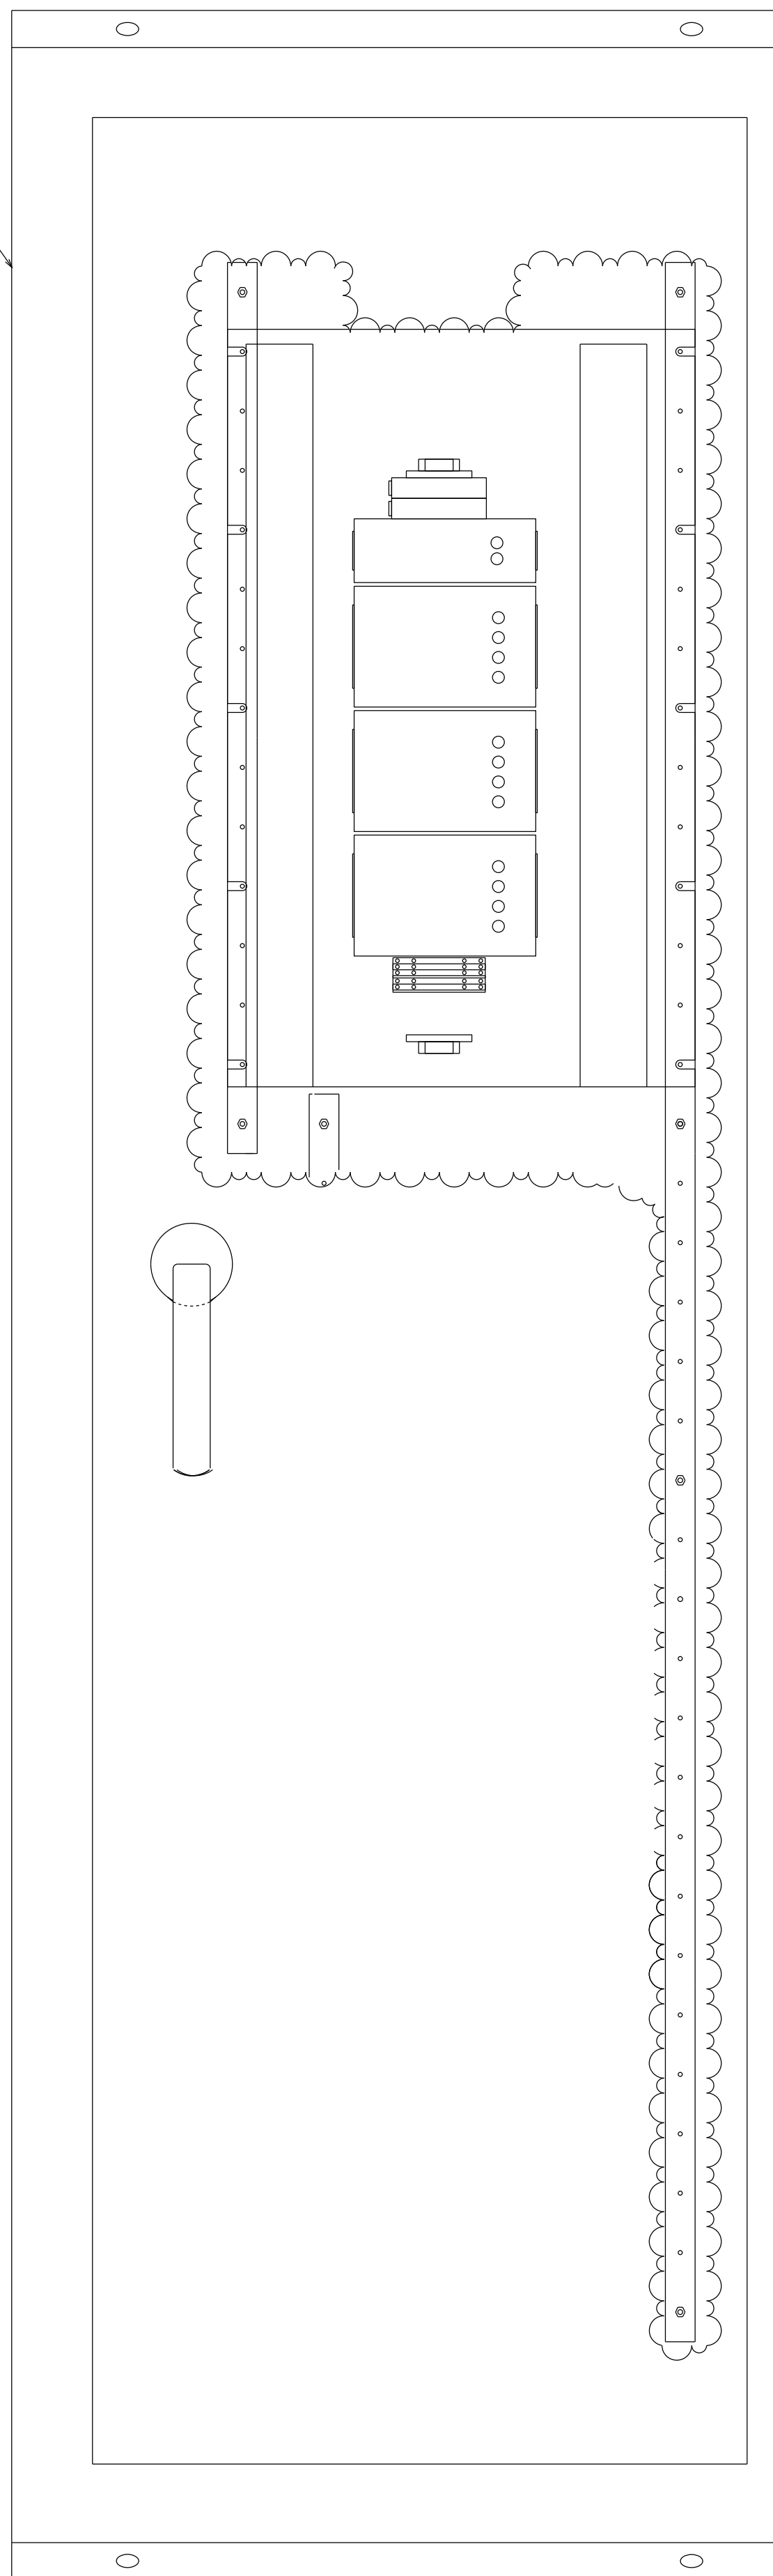

LEFT INTERIOR VIEW

FRONT VIEW


RIGHT INTERIOR VIEW

THIS PRINT IS PROVIDED ON A RESTRICTED BASIS AND IS NOT TO BE USED IN ANY WAY DETRIMENTAL TO SOLAR TURBINES INCORPORATED.			
REVISION HISTORY			
REV	DESCRIPTION	DATE	APPROVED
0	0	0	0
C		04/14/26	S. LOZA

INSTALL IN ACCORDANCE WITH THE NATIONAL
ELECTRICAL CODE (NEC), AND ANY APPLICABLE
LOCAL CODES

BOX: 2953147-100

CATERPILLAR CONFIDENTIAL GREEN							
THIS COPYRIGHTED WORK AND THE INFORMATION HEREIN IS PROPRIETARY TO CATERPILLAR INC., SOLAR TURBINES INCORPORATED, AND/OR SUBSIDIARIES OF EITHER. WITHOUT EXPRESS WRITTEN PERMISSION FROM CATERPILLAR INC. OR SOLAR TURBINES INCORPORATED, ANY COPYING, DISCLOSURE, OR USE EXCEPT THAT FOR WHICH IT IS LOANED, IS PROHIBITED.							
DATA CONTROL LEVEL 1	RELEASE STAMP PD – 4M371	SIZE	CAGE NO.	Solar Turbines <i>A Caterpillar Company</i>	P.O. BOX 85376 San Diego, California 92186-5376		
		D	66195				
		MFG DES ENGINEER	DATE			DRAWING TITLE	
		S. LOZA	01/21/2025				CONTROL,JB72
		DESIGN ENGINEER	DATE				
J. PECACHE		01/21/2025					
PROJECT NAME				SOLARIS ENERGY INFRASTRUCTURE			
				PANEL NO.2875787			
MODEL		DWG NO.			SHT		
CTLMO2 TURBOTRONICS 4		4M371-149448			REV C		
LOC		T:\PROJECT\LAYOU\					
		DWG REV C.1			SHEET 13 OF 20		

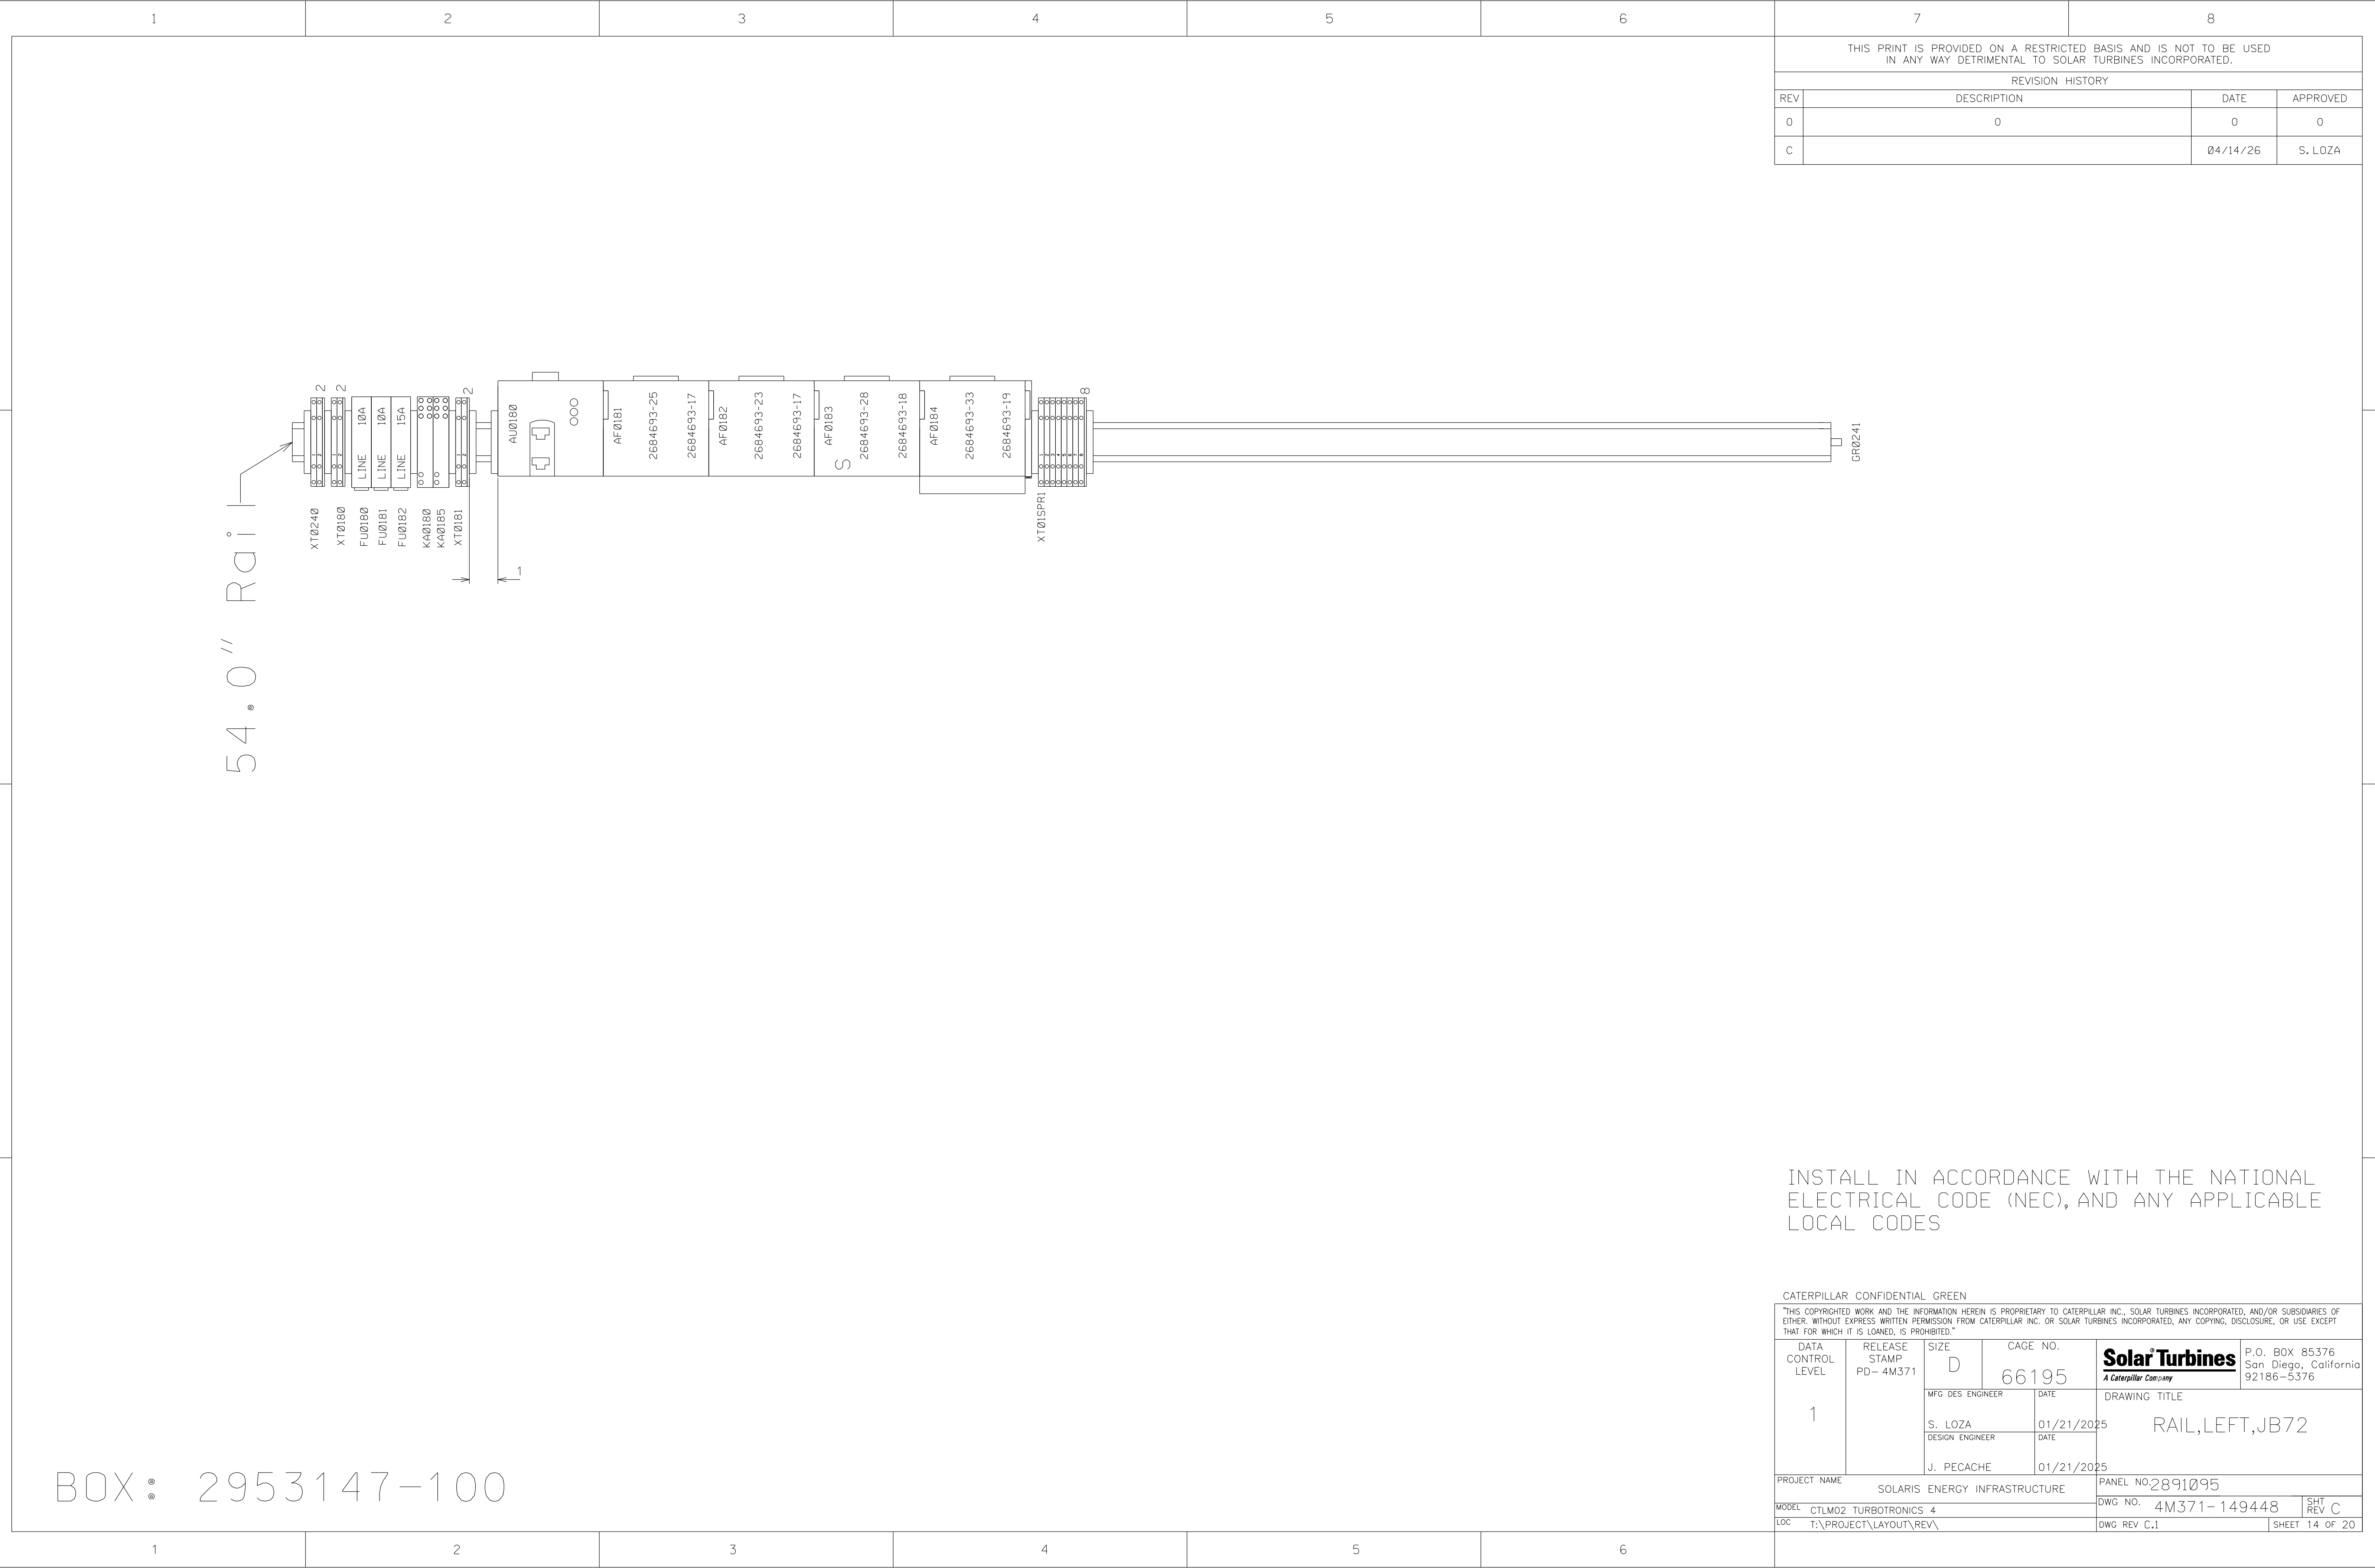

THIS PRINT IS PROVIDED ON A RESTRICTED BASIS AND IS NOT TO BE USED IN ANY WAY DETRIMENTAL TO SOLAR TURBINES INCORPORATED.			
REVISION HISTORY			
REV	DESCRIPTION	DATE	APPROVED
0	0	0	0
C		04/14/26	S. LOZA

ADD "GROUND" LABEL TO ALL
FG TERMINATION POINTS




INSTALL IN ACCORDANCE WITH THE NATIONAL
ELECTRICAL CODE (NEC), AND ANY APPLICABLE
LOCAL CODES

BOX: 2953147-100

CATERPILLAR CONFIDENTIAL GREEN						
"THIS COPYRIGHTED WORK AND THE INFORMATION HEREIN IS PROPRIETARY TO CATERPILLAR INC., SOLAR TURBINES INCORPORATED, AND/OR SUBSIDIARIES OF EITHER. WITHOUT EXPRESS WRITTEN PERMISSION FROM CATERPILLAR INC. OR SOLAR TURBINES INCORPORATED, ANY COPYING, DISCLOSURE, OR USE EXCEPT THAT FOR WHICH IT IS LOANED, IS PROHIBITED."						
DATA CONTROL LEVEL 1	RELEASE STAMP PD- 4M371	SIZE D	CAGE NO. 66195		Solar®Turbines <i>A Caterpillar Company</i> P.O. BOX 85376 San Diego, California 92186-5376	
		MFG DES ENGINEER	DATE	DRAWING TITLE RAIL,RIGHT,JB72		
		S. LOZA	01/21/2025			
		DESIGN ENGINEER	DATE			
		J. PECACHE	01/21/2025			
PROJECT NAME SOLARIS ENERGY INFRASTRUCTURE				PANEL NO.2891103		
MODEL	CTLM02 TURBOTRONICS 4			DWG NO.	4M371- 149448	SHT REV C
OC	T:\PROJECT\LAYOUT\REV\			DWG REV C.1		SHEET 15 OF 20

THIS PRINT IS PROVIDED ON A RESTRICTED BASIS AND IS NOT TO BE USED IN ANY WAY DETRIMENTAL TO SOLAR TURBINES INCORPORATED.			
REVISION HISTORY			
REV	DESCRIPTION	DATE	APPROVED
0	0	0	0
C		04/14/26	S. LOZA

ADD "GROUND" LABEL TO ALL
FG TERMINATION POINTS

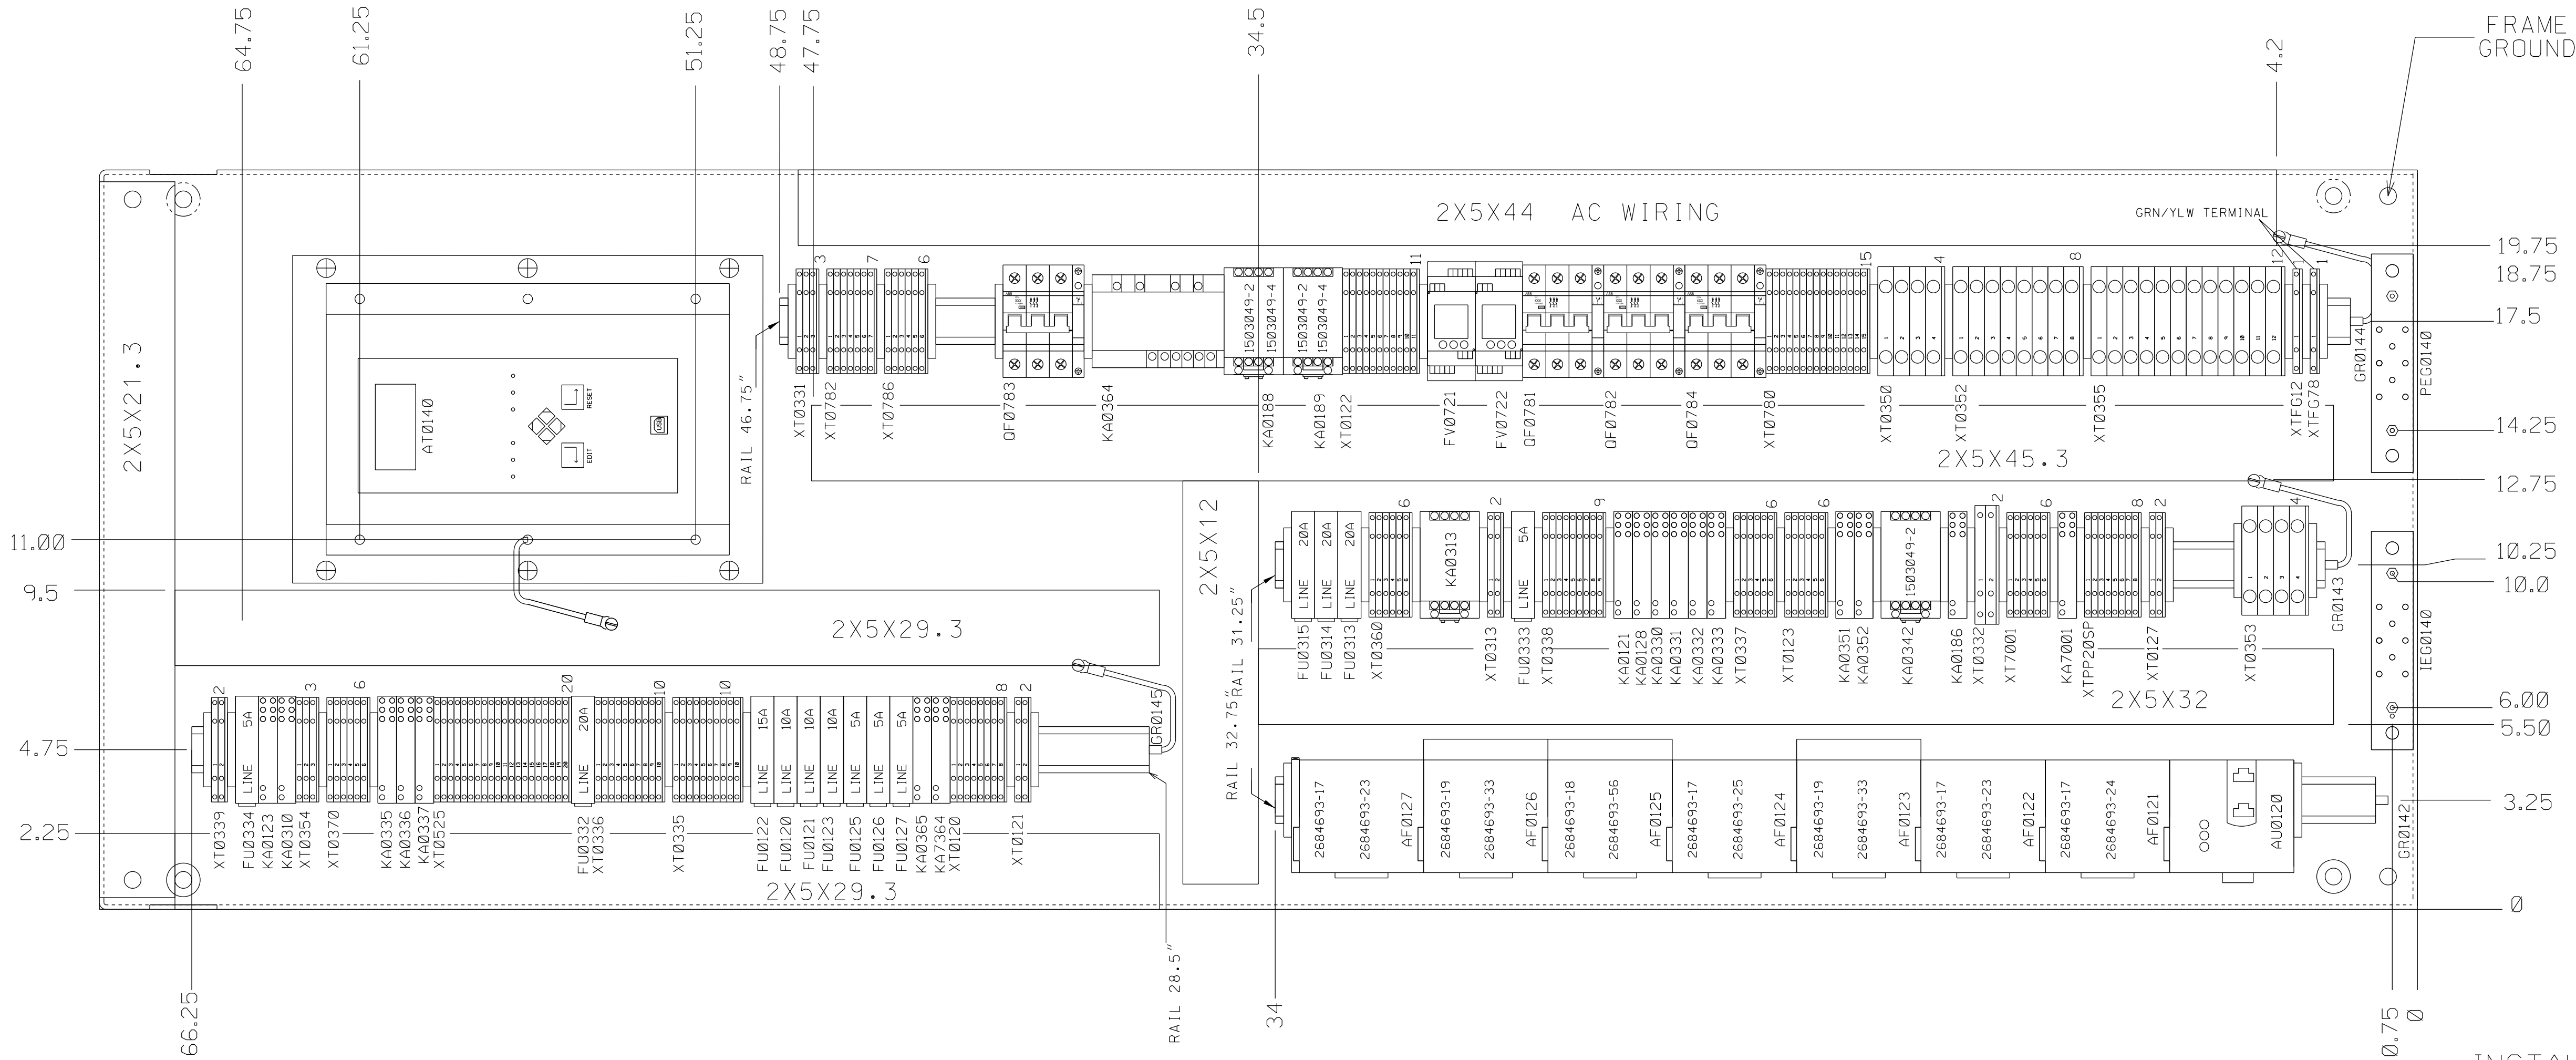

INSTALL IN ACCORDANCE WITH THE NATIONAL
ELECTRICAL CODE (NEC), AND ANY APPLICABLE
LOCAL CODES

PANEL : 1053331-501
BOX : 2953147-100

CATERPILLAR CONFIDENTIAL GREEN						
THIS COPYRIGHTED WORK AND THE INFORMATION HEREIN IS PROPRIETARY TO CATERPILLAR INC., SOLAR TURBINES INCORPORATED, AND/OR SUBSIDIARIES OF EITHER. WITHOUT EXPRESS WRITTEN PERMISSION FROM CATERPILLAR INC. OR SOLAR TURBINES INCORPORATED, ANY COPYING, DISCLOSURE, OR USE EXCEPT THAT FOR WHICH IT IS LOANED, IS PROHIBITED.						
DATA CONTROL LEVEL 1	RELEASE STAMP PD- 4M371	SIZE D	CAGE NO. 66195		Solar Turbines <i>A Caterpillar Company</i> P.O. BOX 85376 San Diego, California 92186-5376	
		MFG DES ENGINEER	DATE	DRAWING TITLE GEN CTRL,JB72		
		S. LOZA	01/21/2025			
		DESIGN ENGINEER	DATE			
		J. PECACHE	01/21/2025			
PROJECT NAME SOLARIS ENERGY INFRASTRUCTURE				PANEL NO 2973868		
MODEL	CTLMO2 TURBOTRONICS 4			DWG NO. 4M371-149448	SHT REV C	
LOC	T:\PROJECT\LAYOUT\REV\			DWG REV C.1	SHEET 17 OF 20	

7		8	
THIS PRINT IS PROVIDED ON A RESTRICTED BASIS AND IS NOT TO BE USED IN ANY WAY DETRIMENTAL TO SOLAR TURBINES INCORPORATED.			
REVISION HISTORY			
REV	DESCRIPTION	DATE	APPROVED
0	0	0	0
C		04/14/26	S. LOZA

ADD "GROUND" LABEL TO ALL
FG TERMINATION POINTS

IF TOP VENT BREATHER INSTALLED,
REMOVE AND INSTALL KIT
156999-4K281

INSTALL IN EXTERIOR
OF THE ENCLOSURE
DOOR

NOTICE
PROVIDES NON-INCENDIVE (NI) CIRCUIT
EXTENSIONS INTO CLASS 1, DIVISION 2,
GROUP D, T3

1033940-508

UA1263

190817-14

UA1210

190817-14

UA1211

190817-14

UA1261

190817-298

UA1262

190817-298

GR1261

FRAME GROUND

INSTALL IN ACCORDANCE WITH THE NATIONAL
ELECTRICAL CODE (NEC), AND ANY APPLICABLE
LOCAL CODES

PANEL: 1058112-1900
BOX: 1057018-32

CATERPILLAR CONFIDENTIAL GREEN

THIS COPYRIGHTED WORK AND THE INFORMATION HEREIN IS PROPRIETARY TO CATERPILLAR INC., SOLAR TURBINES INCORPORATED, AND/OR SUBSIDIARIES OF EITHER. WITHOUT EXPRESS WRITTEN PERMISSION FROM CATERPILLAR INC. OR SOLAR TURBINES INCORPORATED, ANY COPYING, DISCLOSURE, OR USE EXCEPT THAT FOR WHICH IT IS LOANED, IS PROHIBITED.

DATA CONTROL LEVEL 1	RELEASE STAMP PD- 4M371	SIZE D	CAGE NO. 66195		Solar Turbines <i>A Caterpillar Company</i> P.O. BOX 85376 San Diego, California 92186-5376
		MFG DES ENGINEER	DATE	DRAWING TITLE FWD PROX,JB350	
		S. LOZA	01/21/2025		
		DESIGN ENGINEER	DATE		
		J. PECACHE	01/21/2025		
PROJECT NAME SOLARIS ENERGY INFRASTRUCTURE					PANEL NO.2983836
MODEL	CTLMO2 TURBOTRONICS 4				DWG NO. 4M371- 149448
LOC	T:\PROJECT\LAYOUT\REV\				SHT REV C
					DWG REV C.1
					SHEET 18 OF 20

