

A.1_M.2

Updated position of ground to be at top of the rail


Nomar Lopez d67755
03-31-26

THIS PRINT IS PROVIDED ON A RESTRICTED BASIS AND IS NOT TO BE USED IN ANY WAY DETRIMENTAL TO SOLAR TURBINES INCORPORATED.			
REVISION HISTORY			
REV	DESCRIPTION	DATE	APPROVED
734	T:\149332\Rev380\1058140-441.dwg	6/17/2015	A. DANG
A.1_M.2		03/31/26	N. LOPEZ

A.1_M.1

Updated numbering of sheets for this CB project.

Nomar Lopez d67755
02-26-26

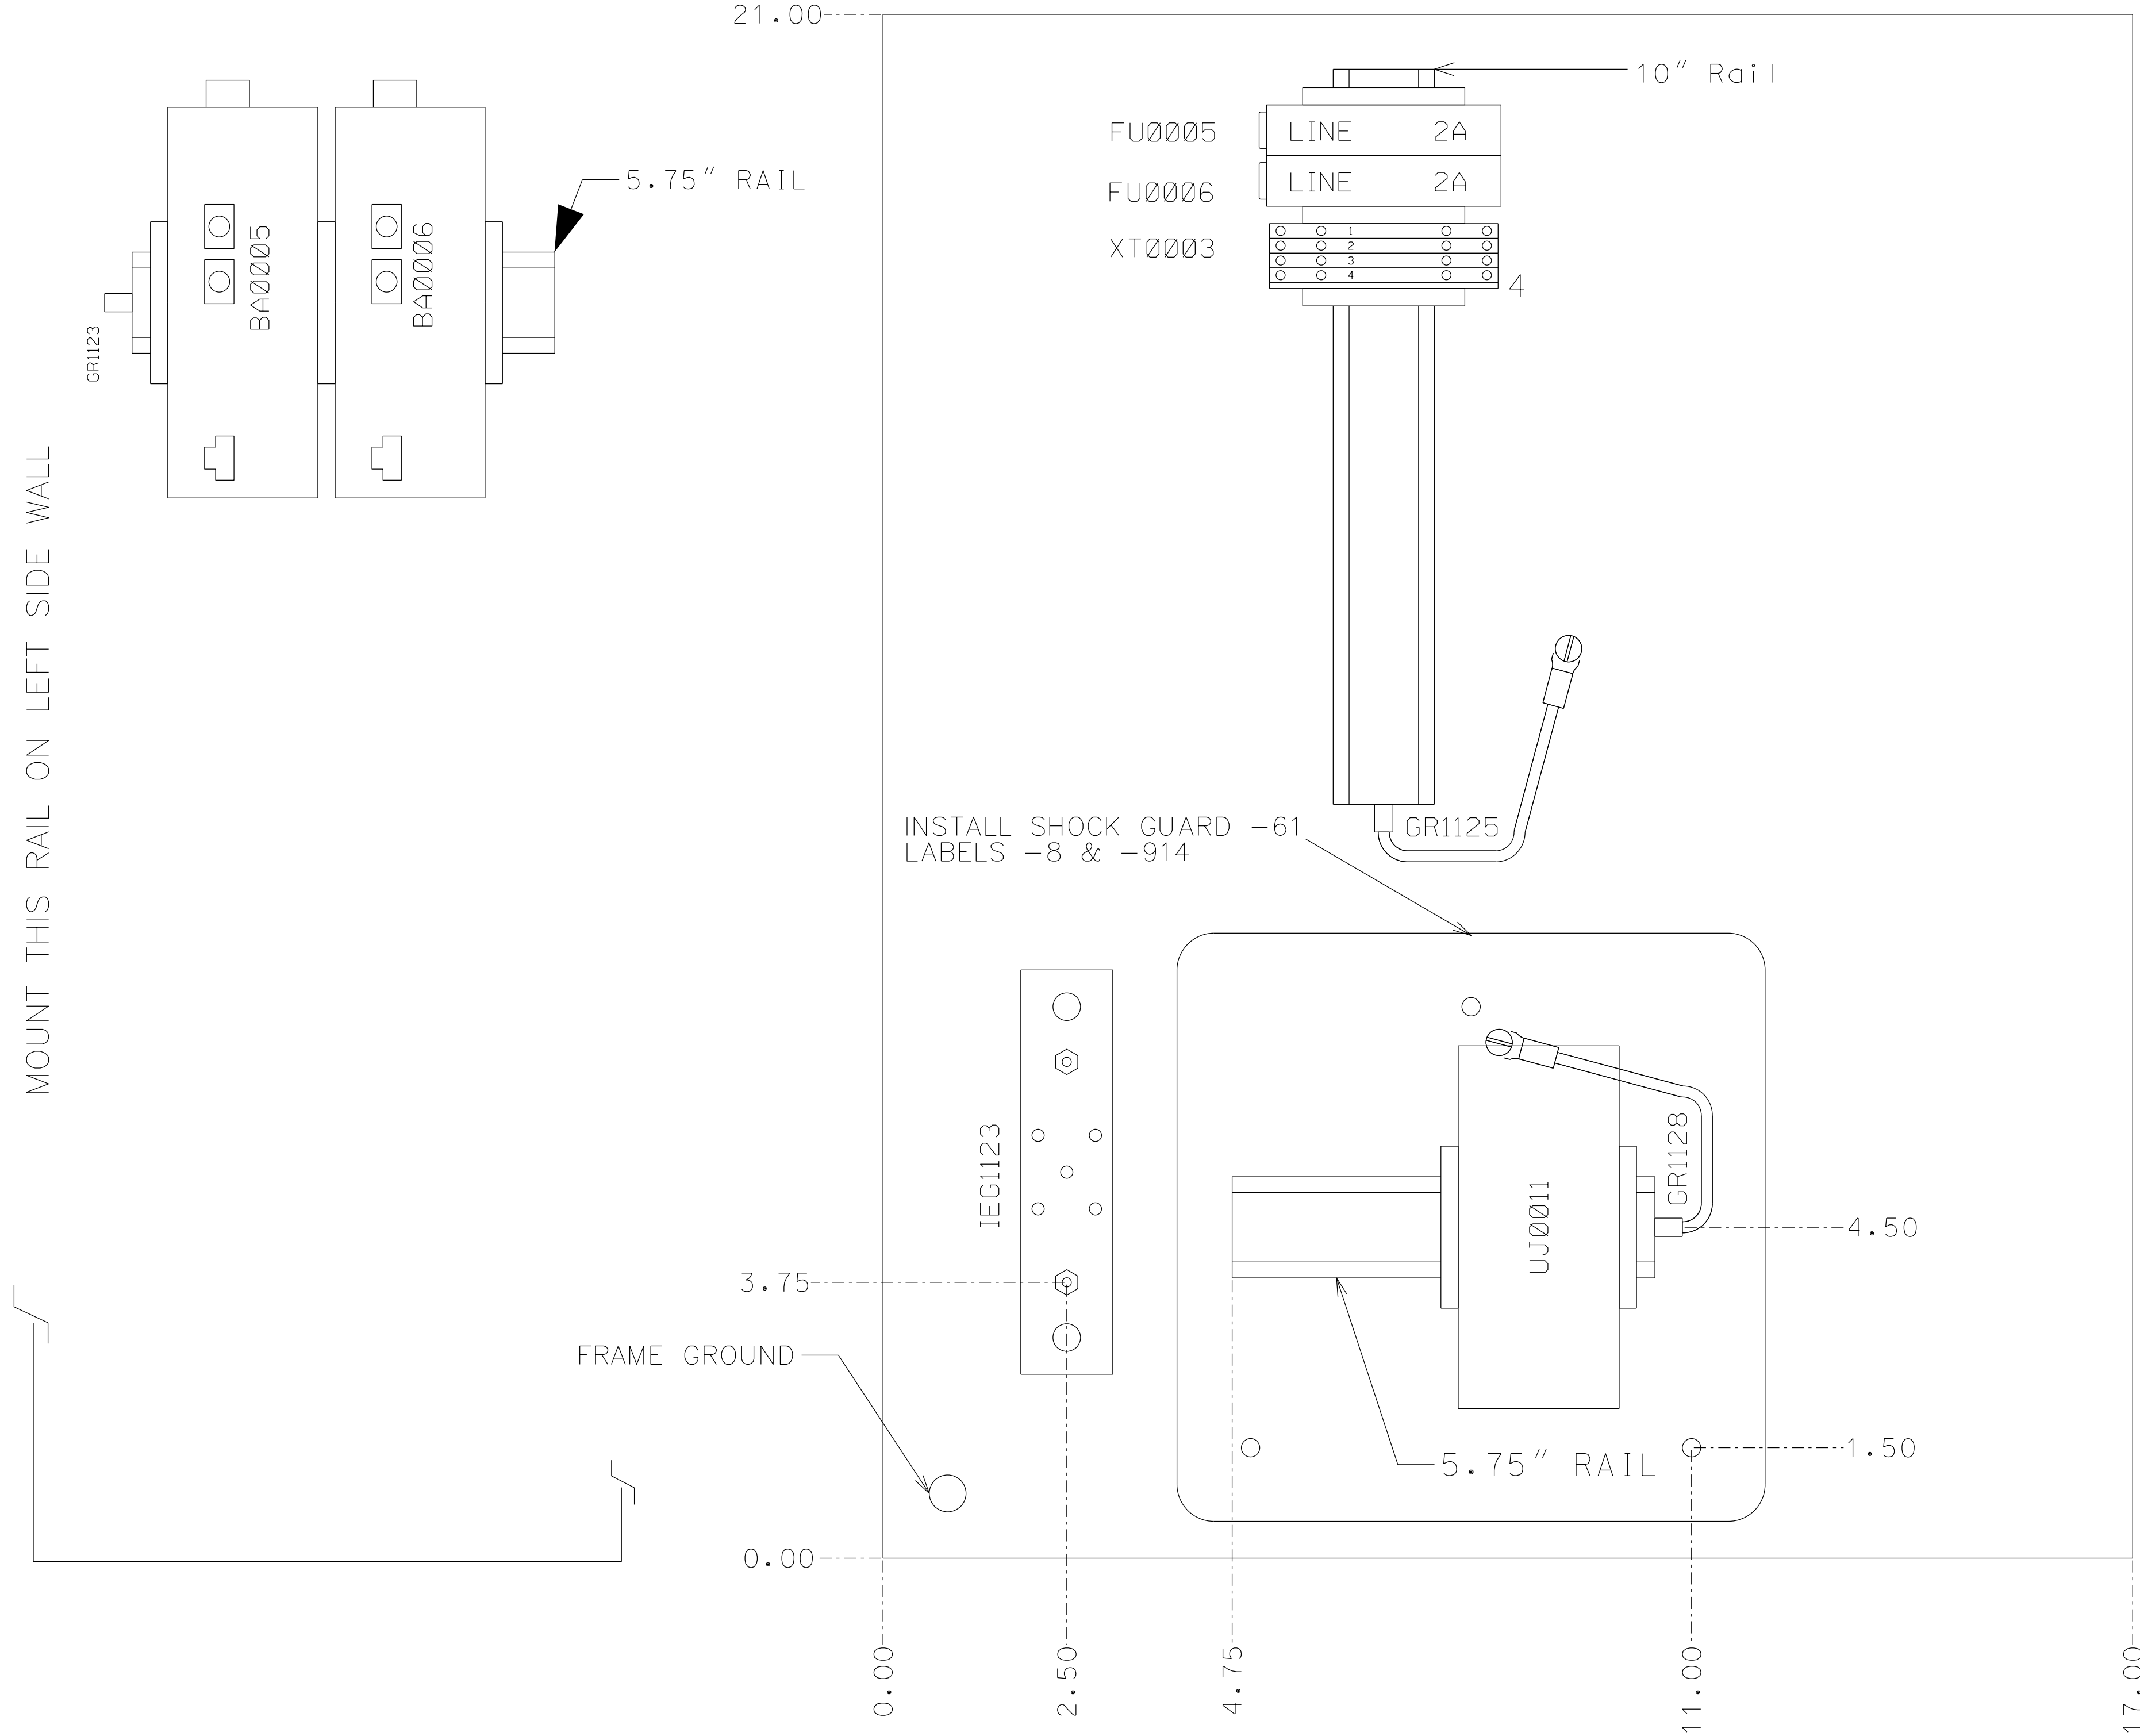

BUILD BOX
UNDER "CB" PID

PANEL: 1058112-2300
BOX: 1054596-50

CATERPILLAR CONFIDENTIAL GREEN							
THIS COPYRIGHTED WORK AND THE INFORMATION HEREIN IS PROPRIETARY TO CATERPILLAR INC., SOLAR TURBINES INCORPORATED, AND/OR SUBSIDIARIES OF EITHER. WITHOUT EXPRESS WRITTEN PERMISSION FROM CATERPILLAR INC. OR SOLAR TURBINES INCORPORATED, ANY COPYING, DISCLOSURE, OR USE EXCEPT THAT FOR WHICH IT IS LOANED, IS PROHIBITED."							
DATA CONTROL LEVEL 1	RELEASE STAMP PD- 4M891	SIZE D	CAGE NO. 66195		Solar²Turbines <i>A Caterpillar Company</i>	P.O. BOX 85376 San Diego, California 92186-5376	
		MFG DES ENGINEER	DATE				DRAWING TITLE VFD MEDIA CONVERTER JB1123
		N. LOPEZ	7/02/2025				
		DESIGN ENGINEER	DATE				
		J. SHORTER	7/02/2025				
PROJECT NAME VOLTAGRID DATA CENTER PROJECT			PANEL NO:1095902				
MODEL LOC	CTLM02 TURBOTRONICS 4 T:\PROJECT\LAYOUT\REV\			DWG NO. DWG REV	4M891- 149419 A.1_M.2	SHT REV	A.1.M.2
				SHEET 1 OF 9			